


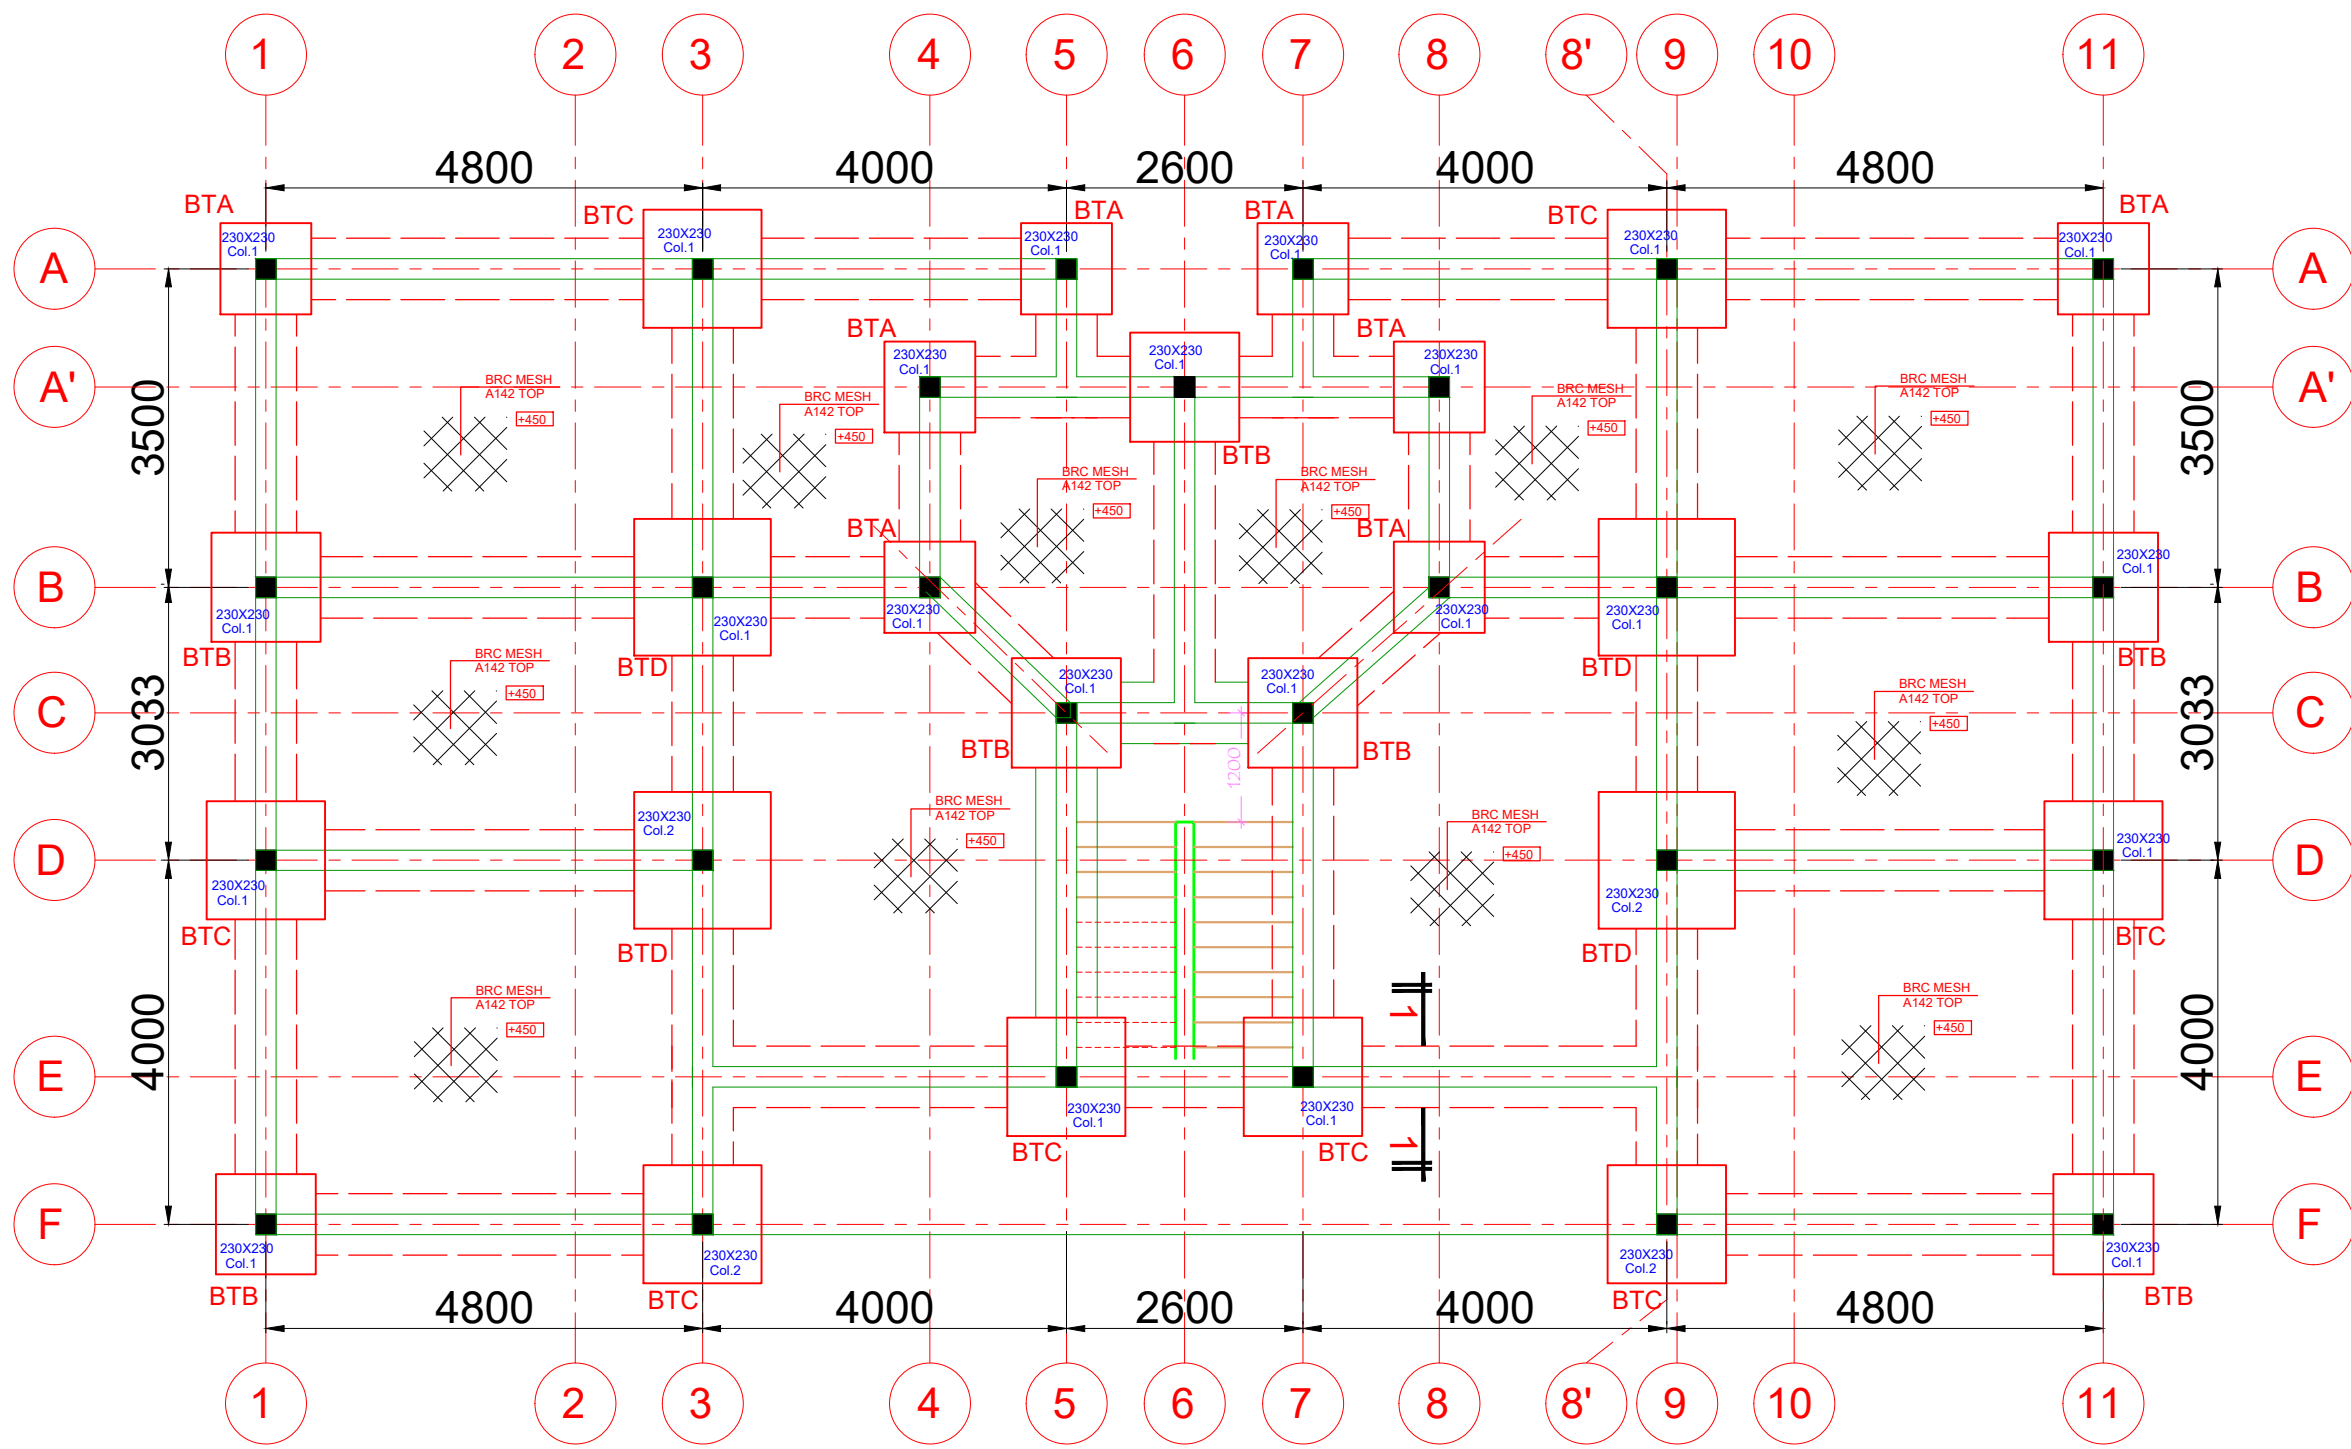

### Notes

1. Only figured dimensions are to be taken
2. This drawing should be read in conjunction with all other architect's drawings
3. Concrete to be in grade 25 and attained a compressive strength of 25 N/mm<sup>2</sup> at 28 days  
Maximum aggregate size to be 19mm
4. For other notes see general notes and specifications.
5. Maximum concrete cover to reinforcement as BS 4449.  
Slab - 15mm  
Beam - 30mm  
Column- 40mm  
Foundation- 50mm
6. The foundation has been designed with soil bearing capacity of 120kn/m<sup>2</sup>.
7. We [the Engineers or/and the firm] are only liable for works supervised by us.  
Our written approval must therefore be obtained for all stages of work.



WUDIL

ProjectTitle:

PROPOSED RESIDENTIAL  
DEVELOPMENT AT PLOT NO.298  
BADAWA NASARAWA.L.G.A  
KANO STATE

Drawing Title:

| TYPE | SIZE              | No. |
|------|-------------------|-----|
| BTA  | 1000 X 1000 X 350 | 8   |
| BTB  | 1200 X 1200 X 350 | 7   |
| BTC  | 1300 X 1300 X 350 | 8   |
| BTD  | 1500 X 1500 X 350 | 4   |

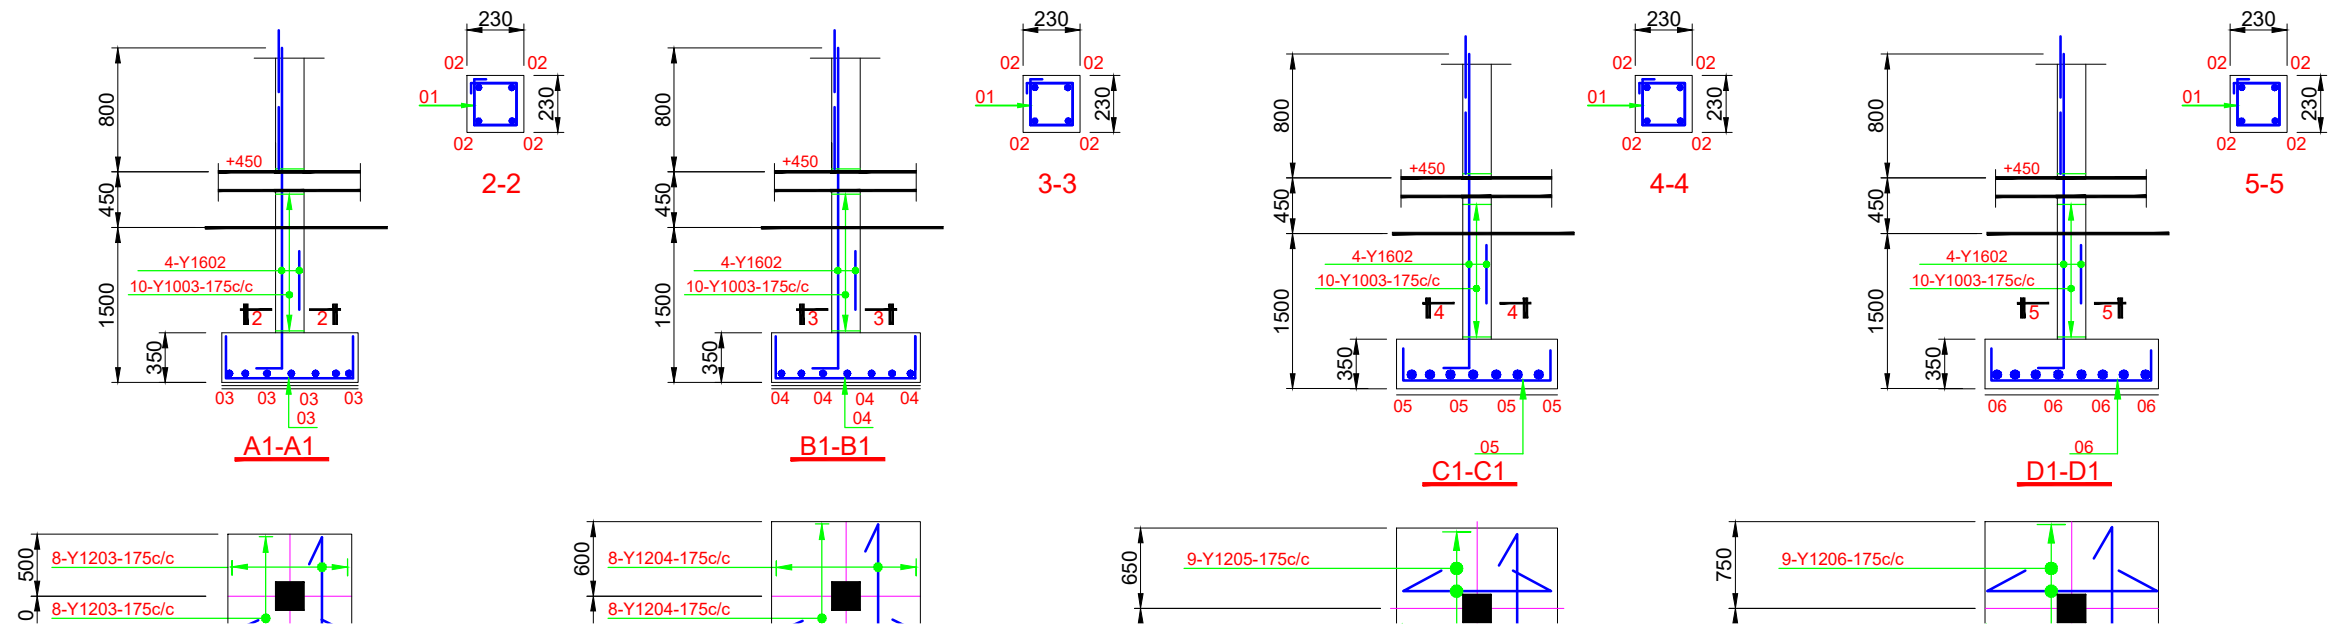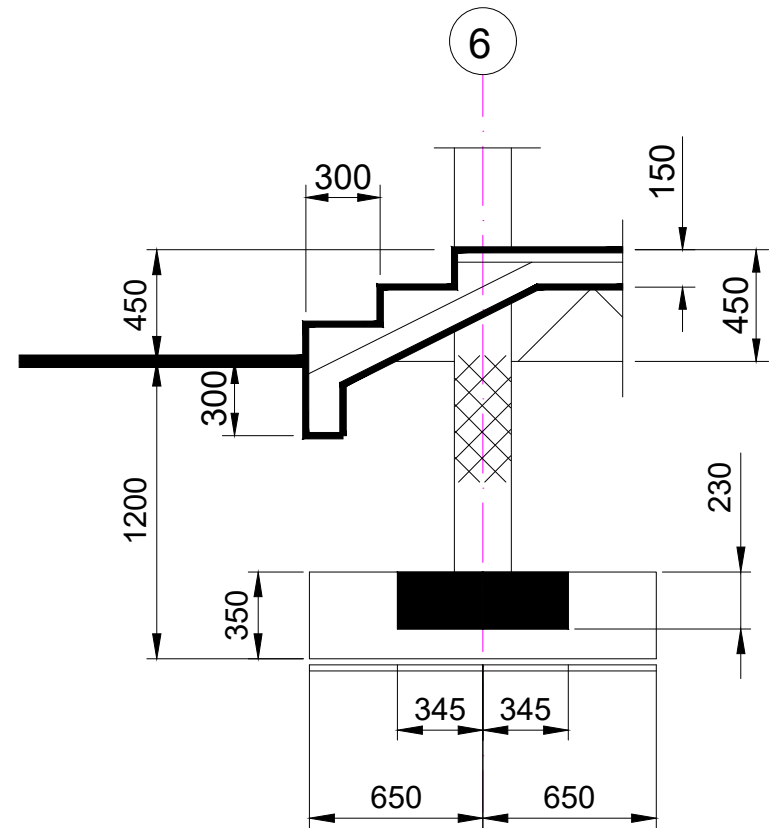

1. Only figured dimensions are to be taken
2. This drawing should be read in conjunction with all other architect's drawings
3. Concrete to be in grade 25 and attained a compressive strength of 25 N/mm<sup>2</sup> at 28 days  
Maximum aggregate size to be 19mm
4. For other notes see general notes and specifications.
5. Maximum concrete cover to reinforcement as BS 4449.  
Slab - 15mm  
follows:- Beam - 30mm  
Column- 40mm  
Foundation- 50mm
6. The foundation has been designed with soil bearing capacity of 120kn/m<sup>2</sup>.
7. We [the Engineers or/and the firm] are only liable for works supervised by us. Our written approval must therefore be obtained for all stages of work.

- 
- 



WUDIL

---

ProjectTitle:

PROPOSED RESIDENTIAL  
DEVELOPMENT AT PLOT NO.298  
BADAWA NASARAWA.L.G.A  
KANO STATE

Drawing Title:

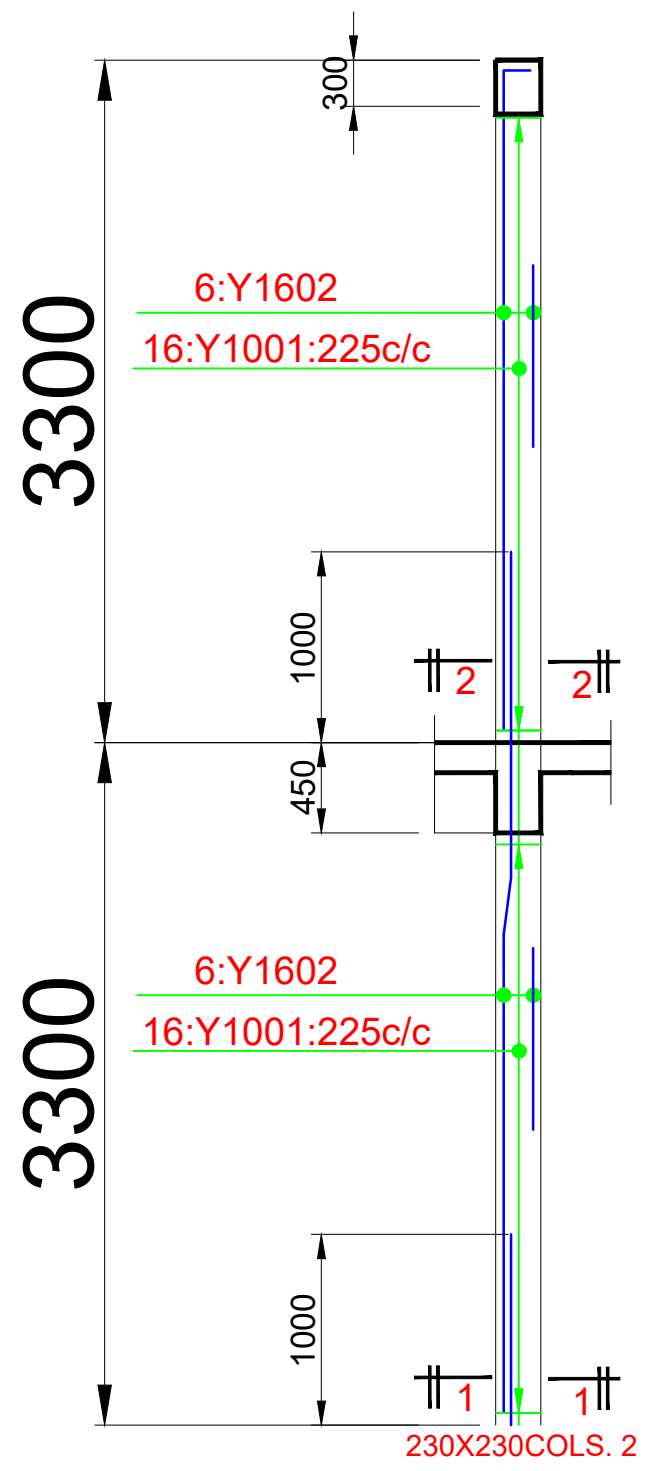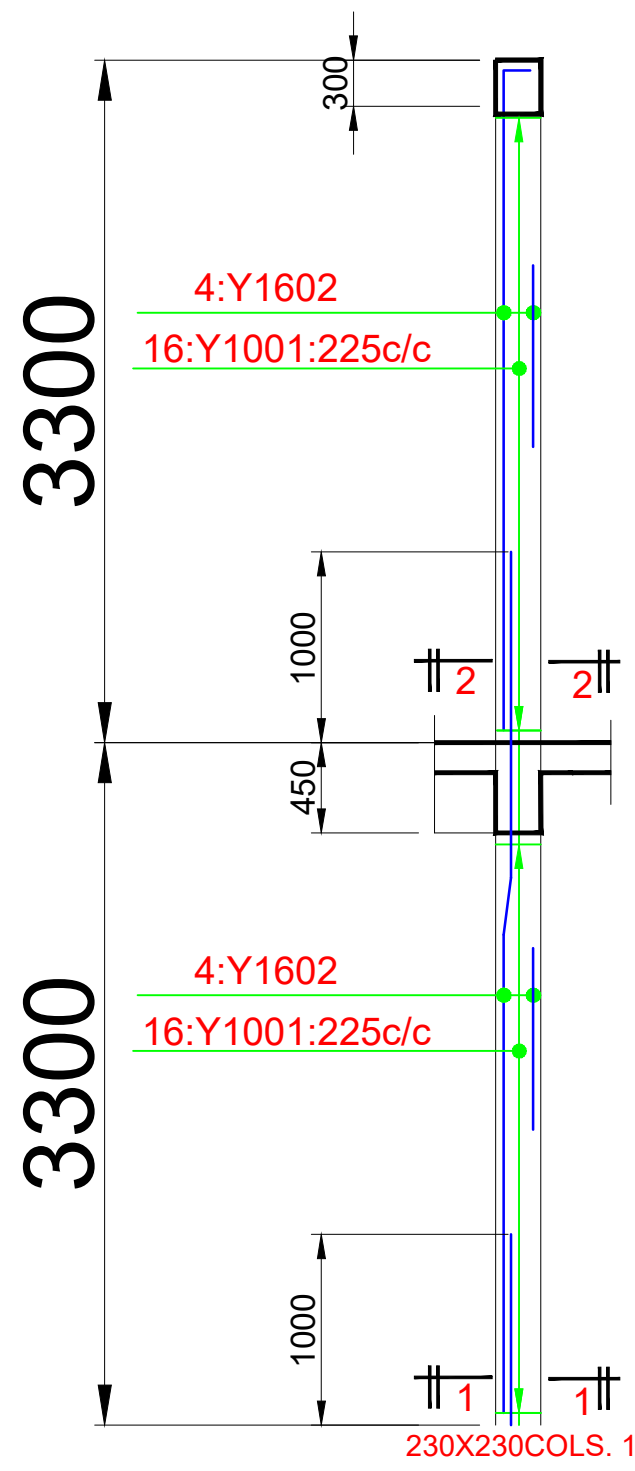

## Notes

1. Only figured dimensions are to be taken
2. This drawing should be read in conjunction with all other architect's drawings
3. Concrete to be in grade 25 and attained a compressive strength of 25 N/mm<sup>2</sup> at 28 days  
Maximum aggregate size to be 19mm
4. For other notes see general notes and specifications.
5. Maximum concrete cover to reinforcement as BS 4449.  
Slab - 15mm  
Beam - 30mm  
Column- 40mm  
Foundation- 50mm
6. The foundation has been designed with soil bearing capacity of 120kn/m<sup>2</sup>.
7. We [the Engineers or/and the firm] are only liable for works supervised by us. Our written approval must therefore be obtained for all stages of work.

:

WUDIL

ProjectTitle:

PROPOSED RESIDENTIAL  
DEVELOPMENT AT PLOT NO.298  
BADAWA NASARAWA.L.G.A  
KANO STATE

Drawing Title: