




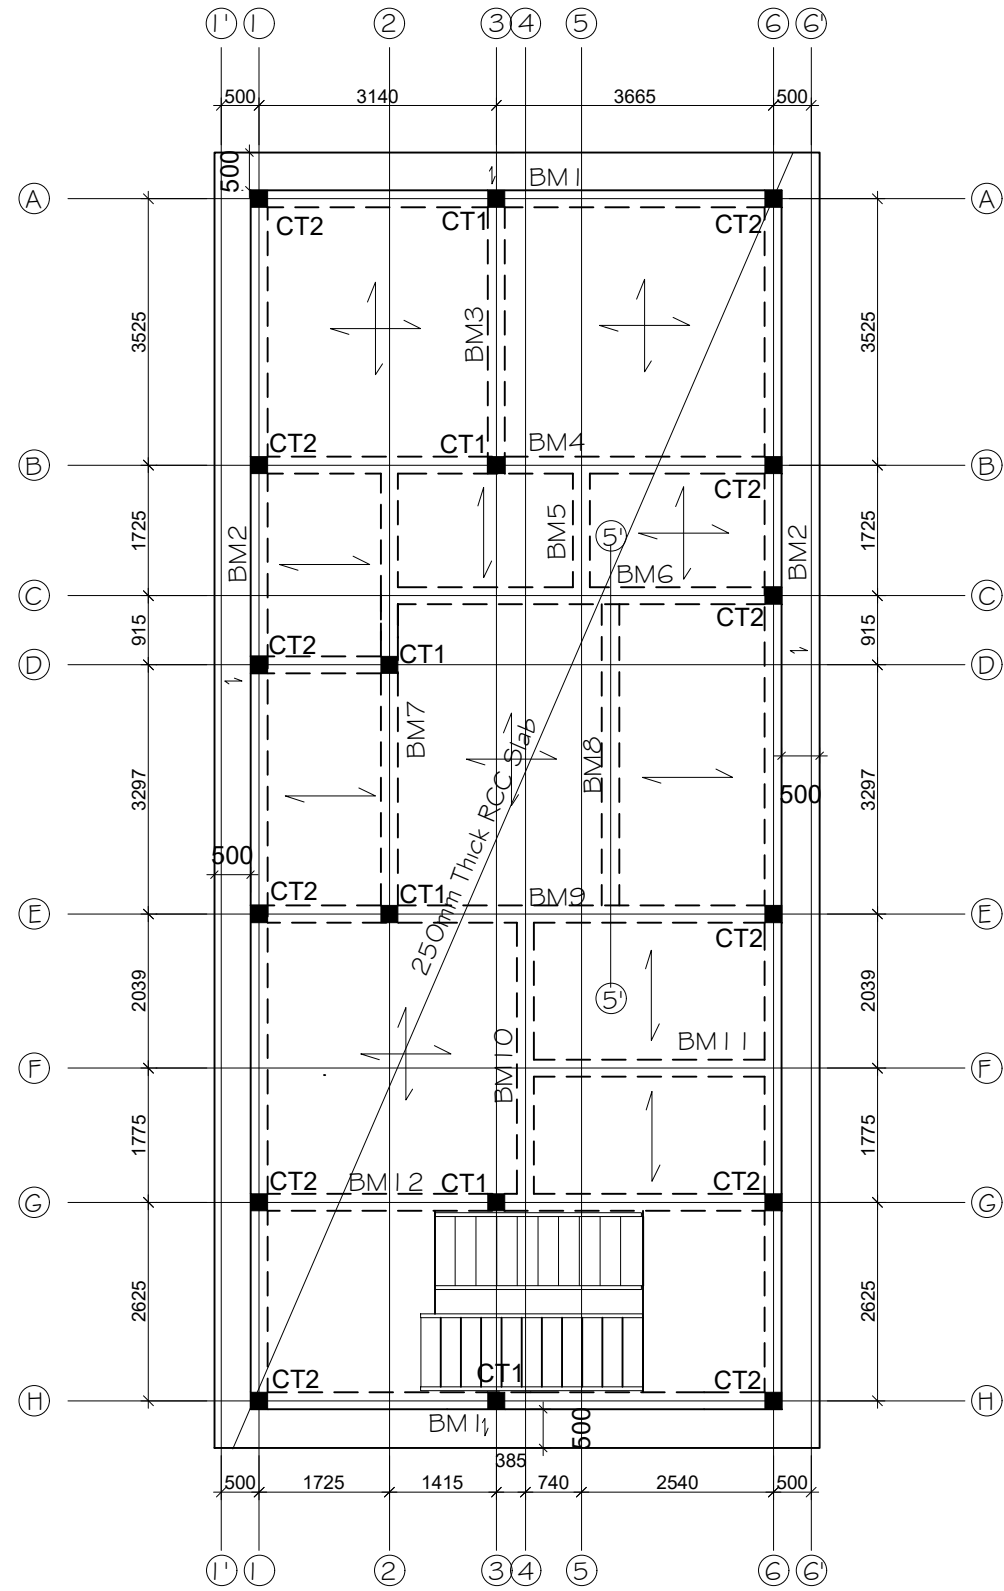

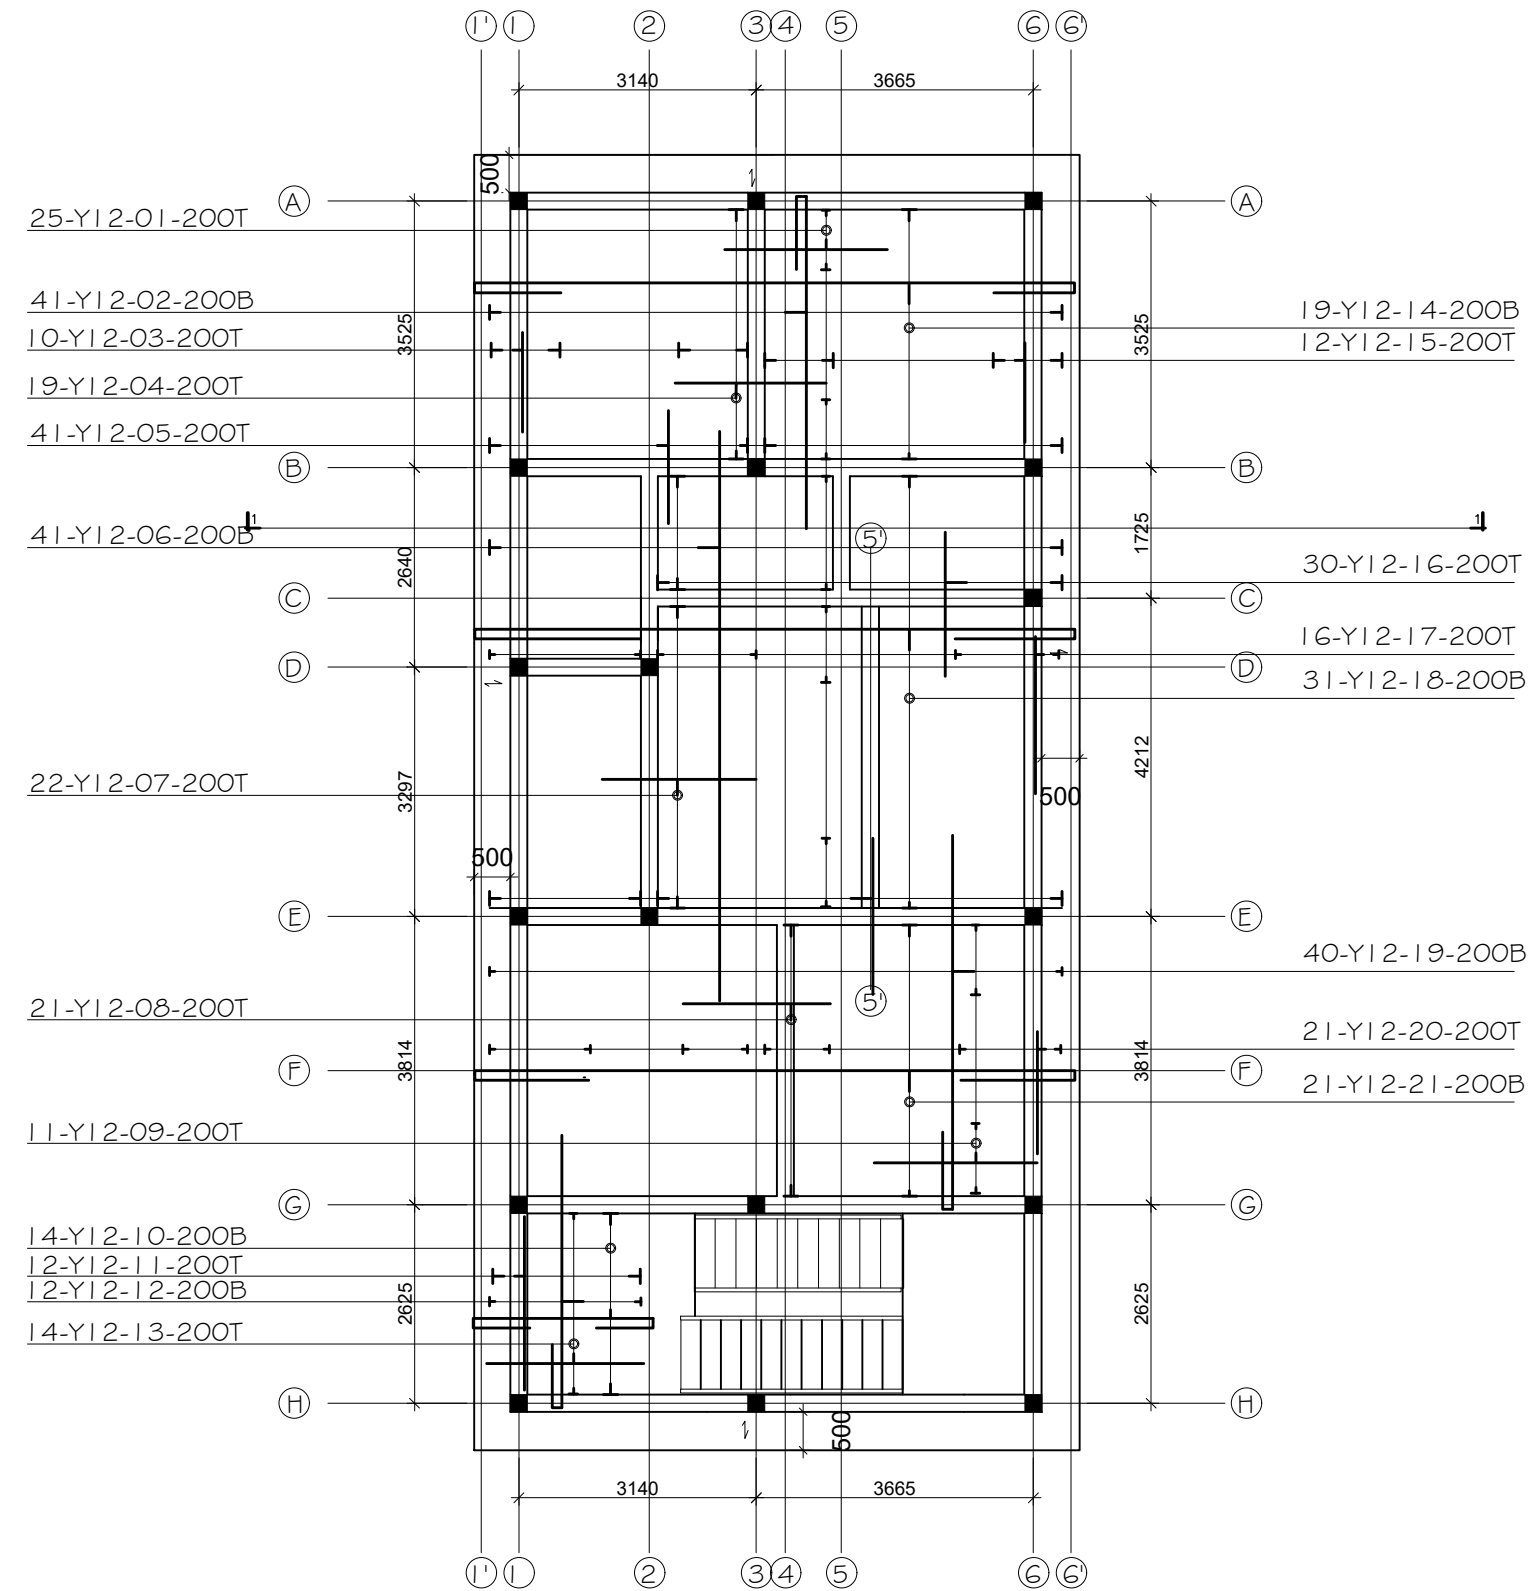

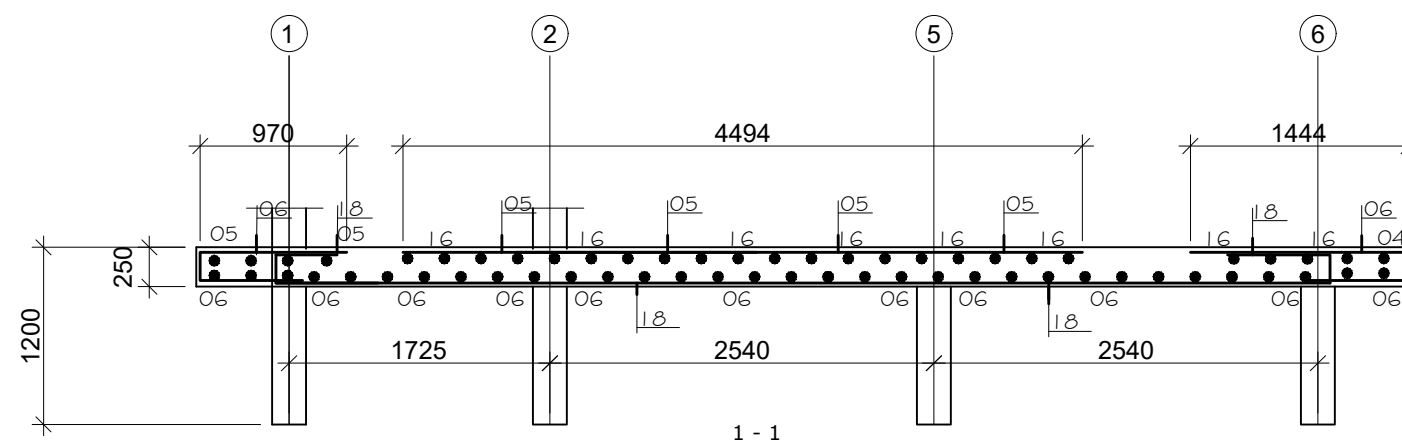

RAFT FOUNDATION SLAB SECTION