




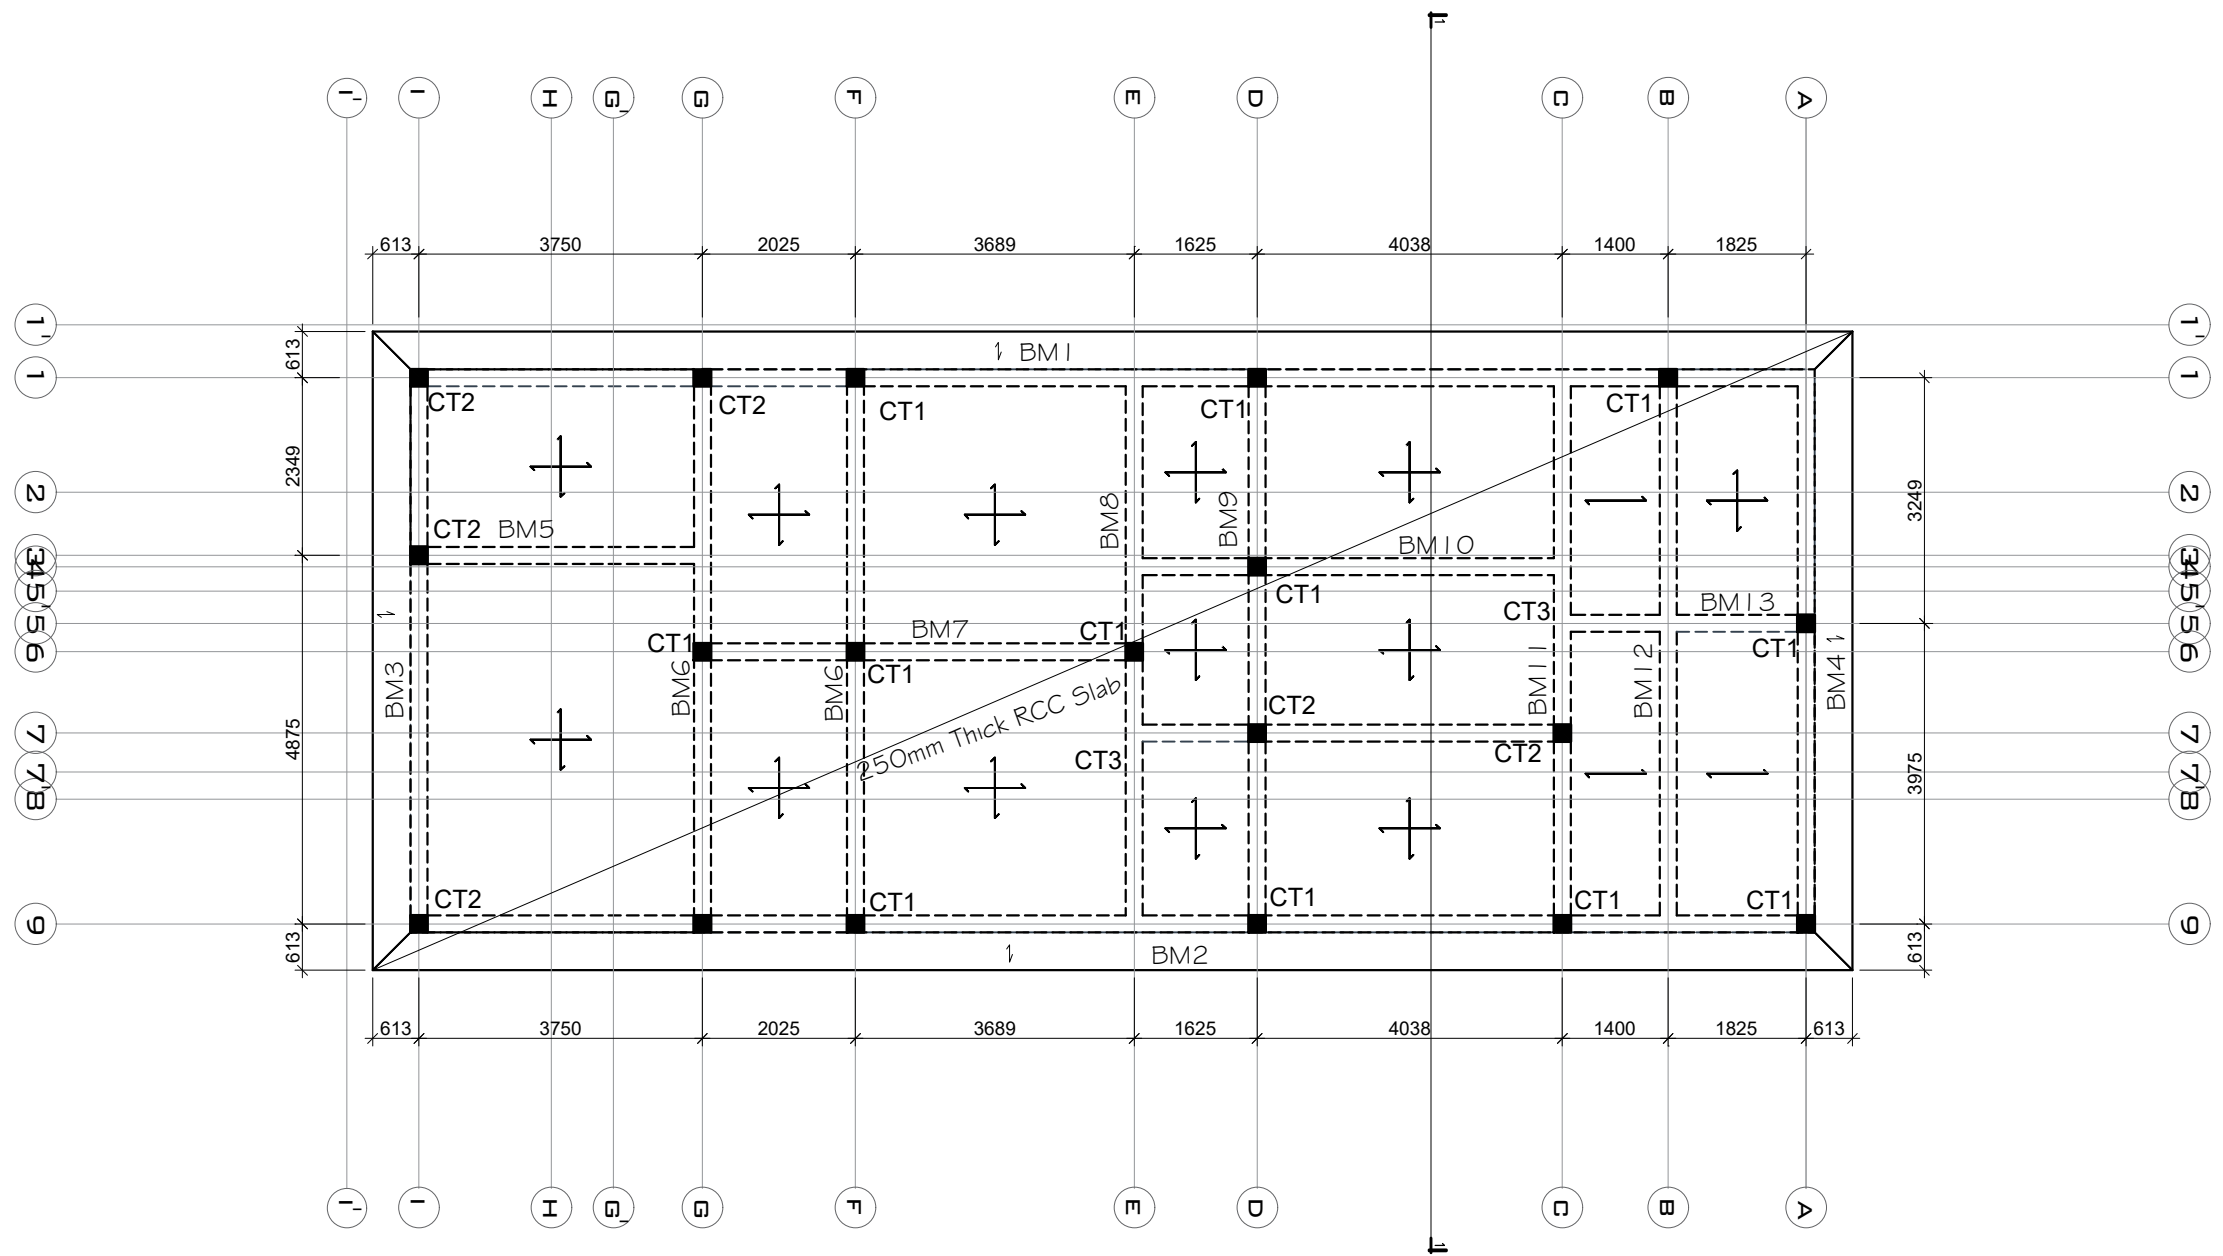

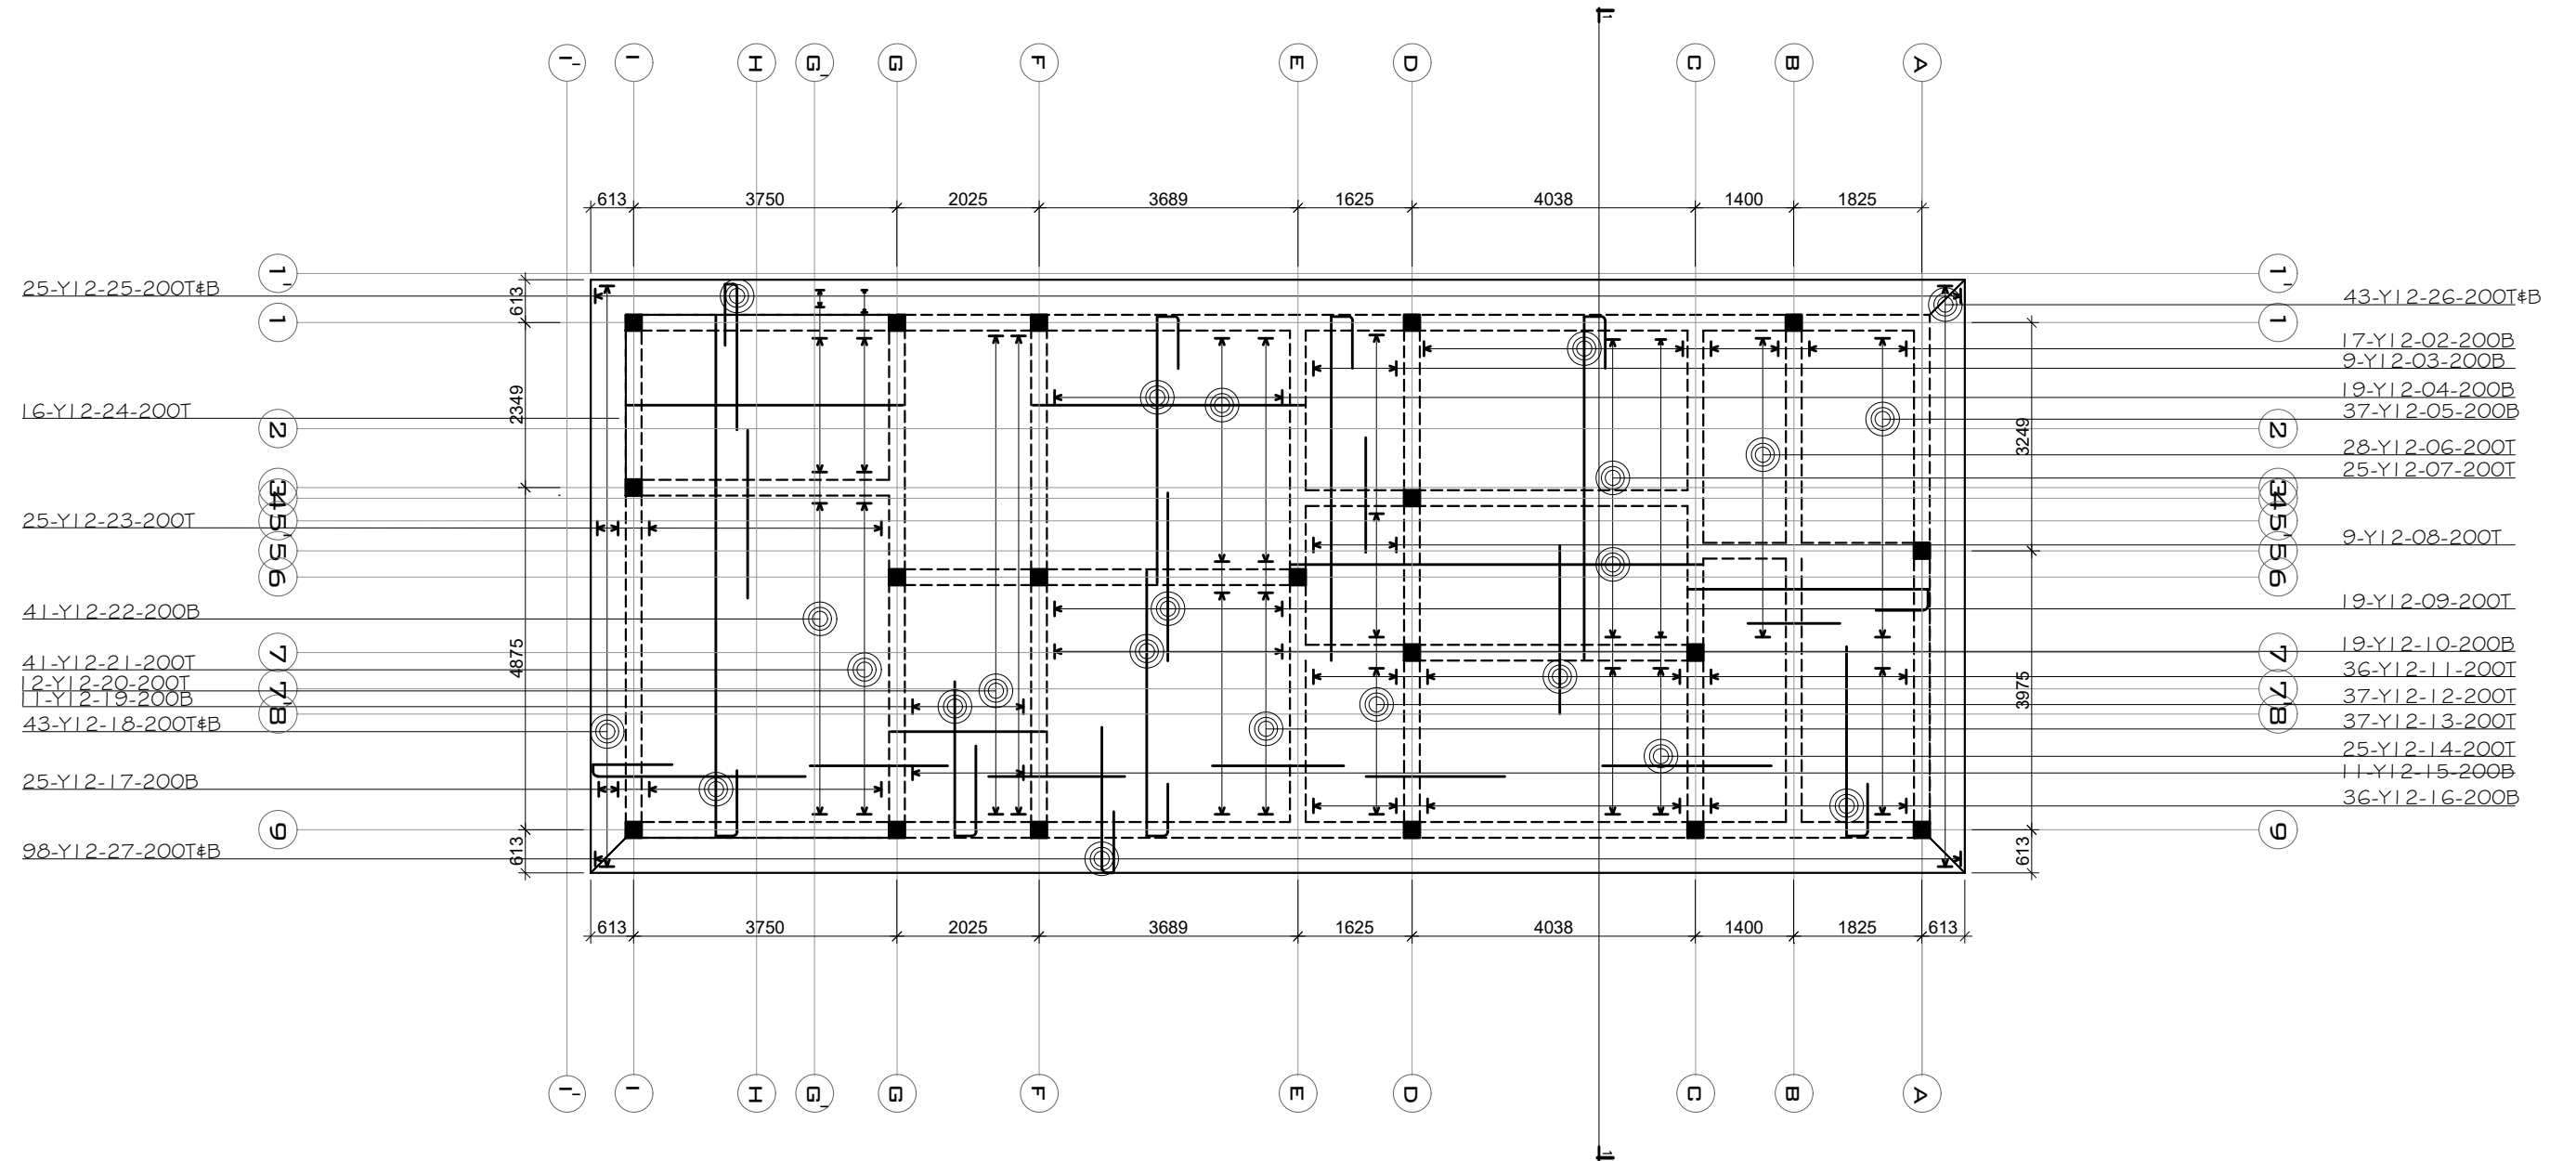

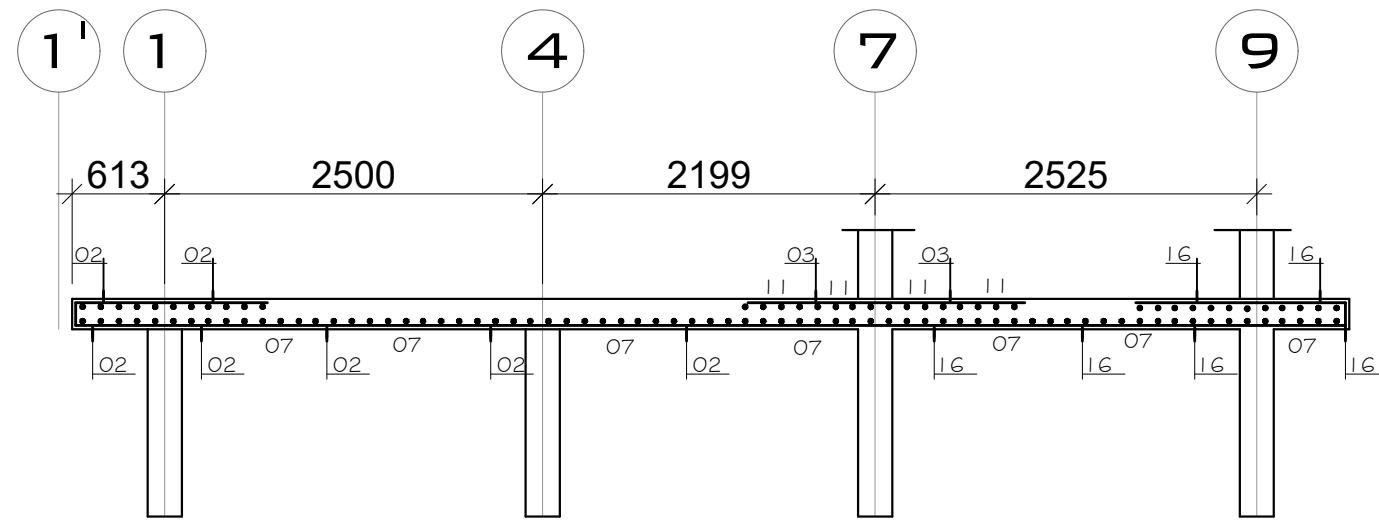

1 - 1

RAFT FOUNDATION SLAB SECTION