



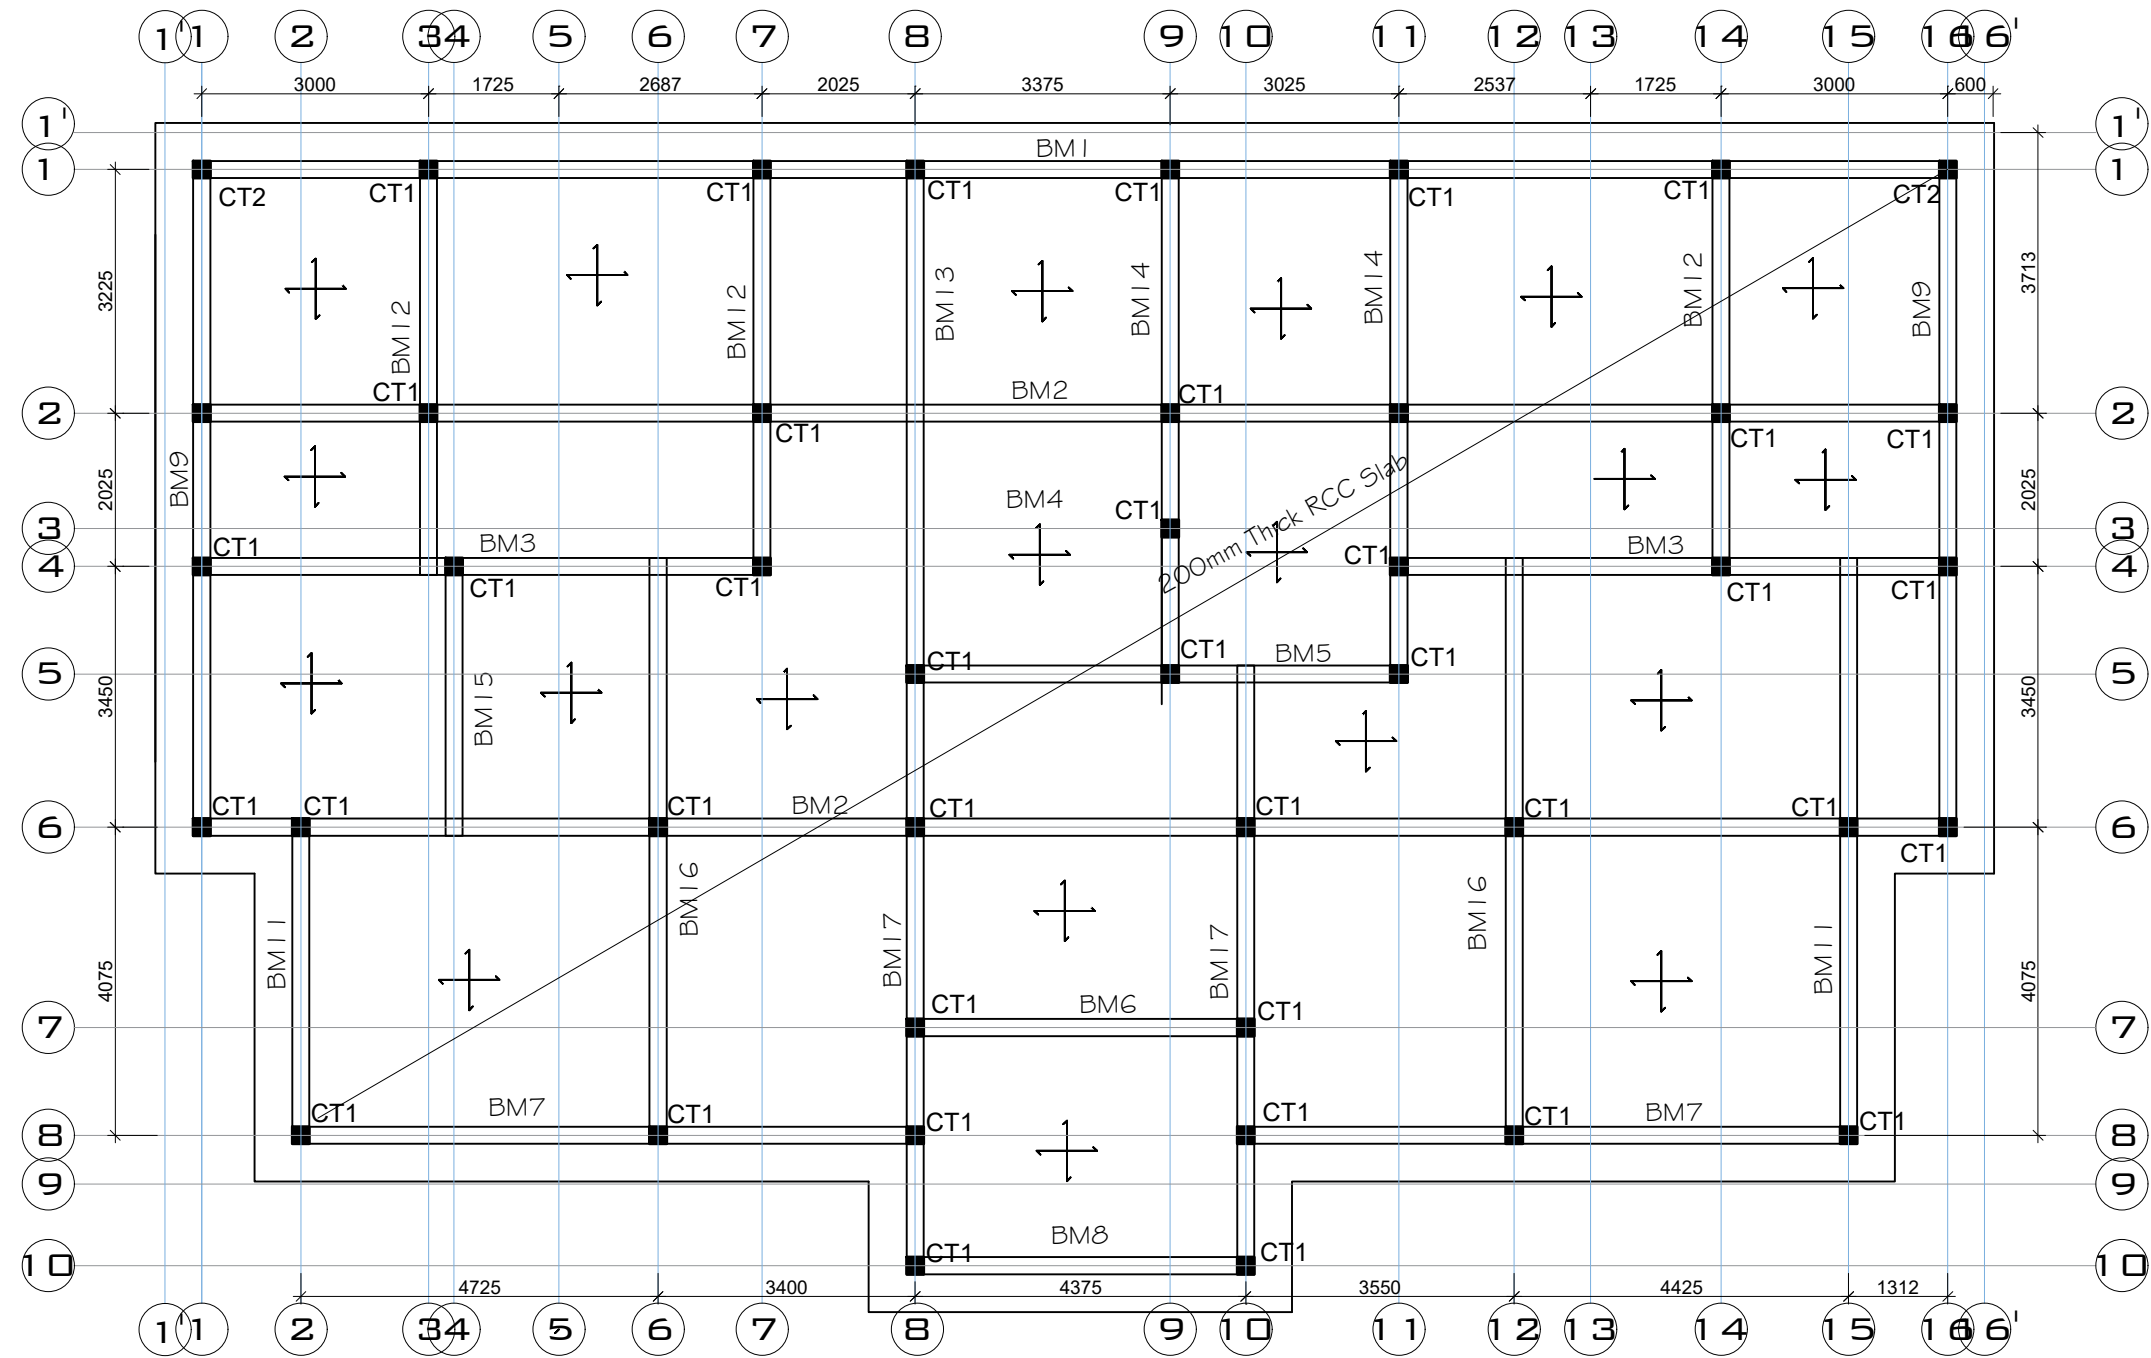


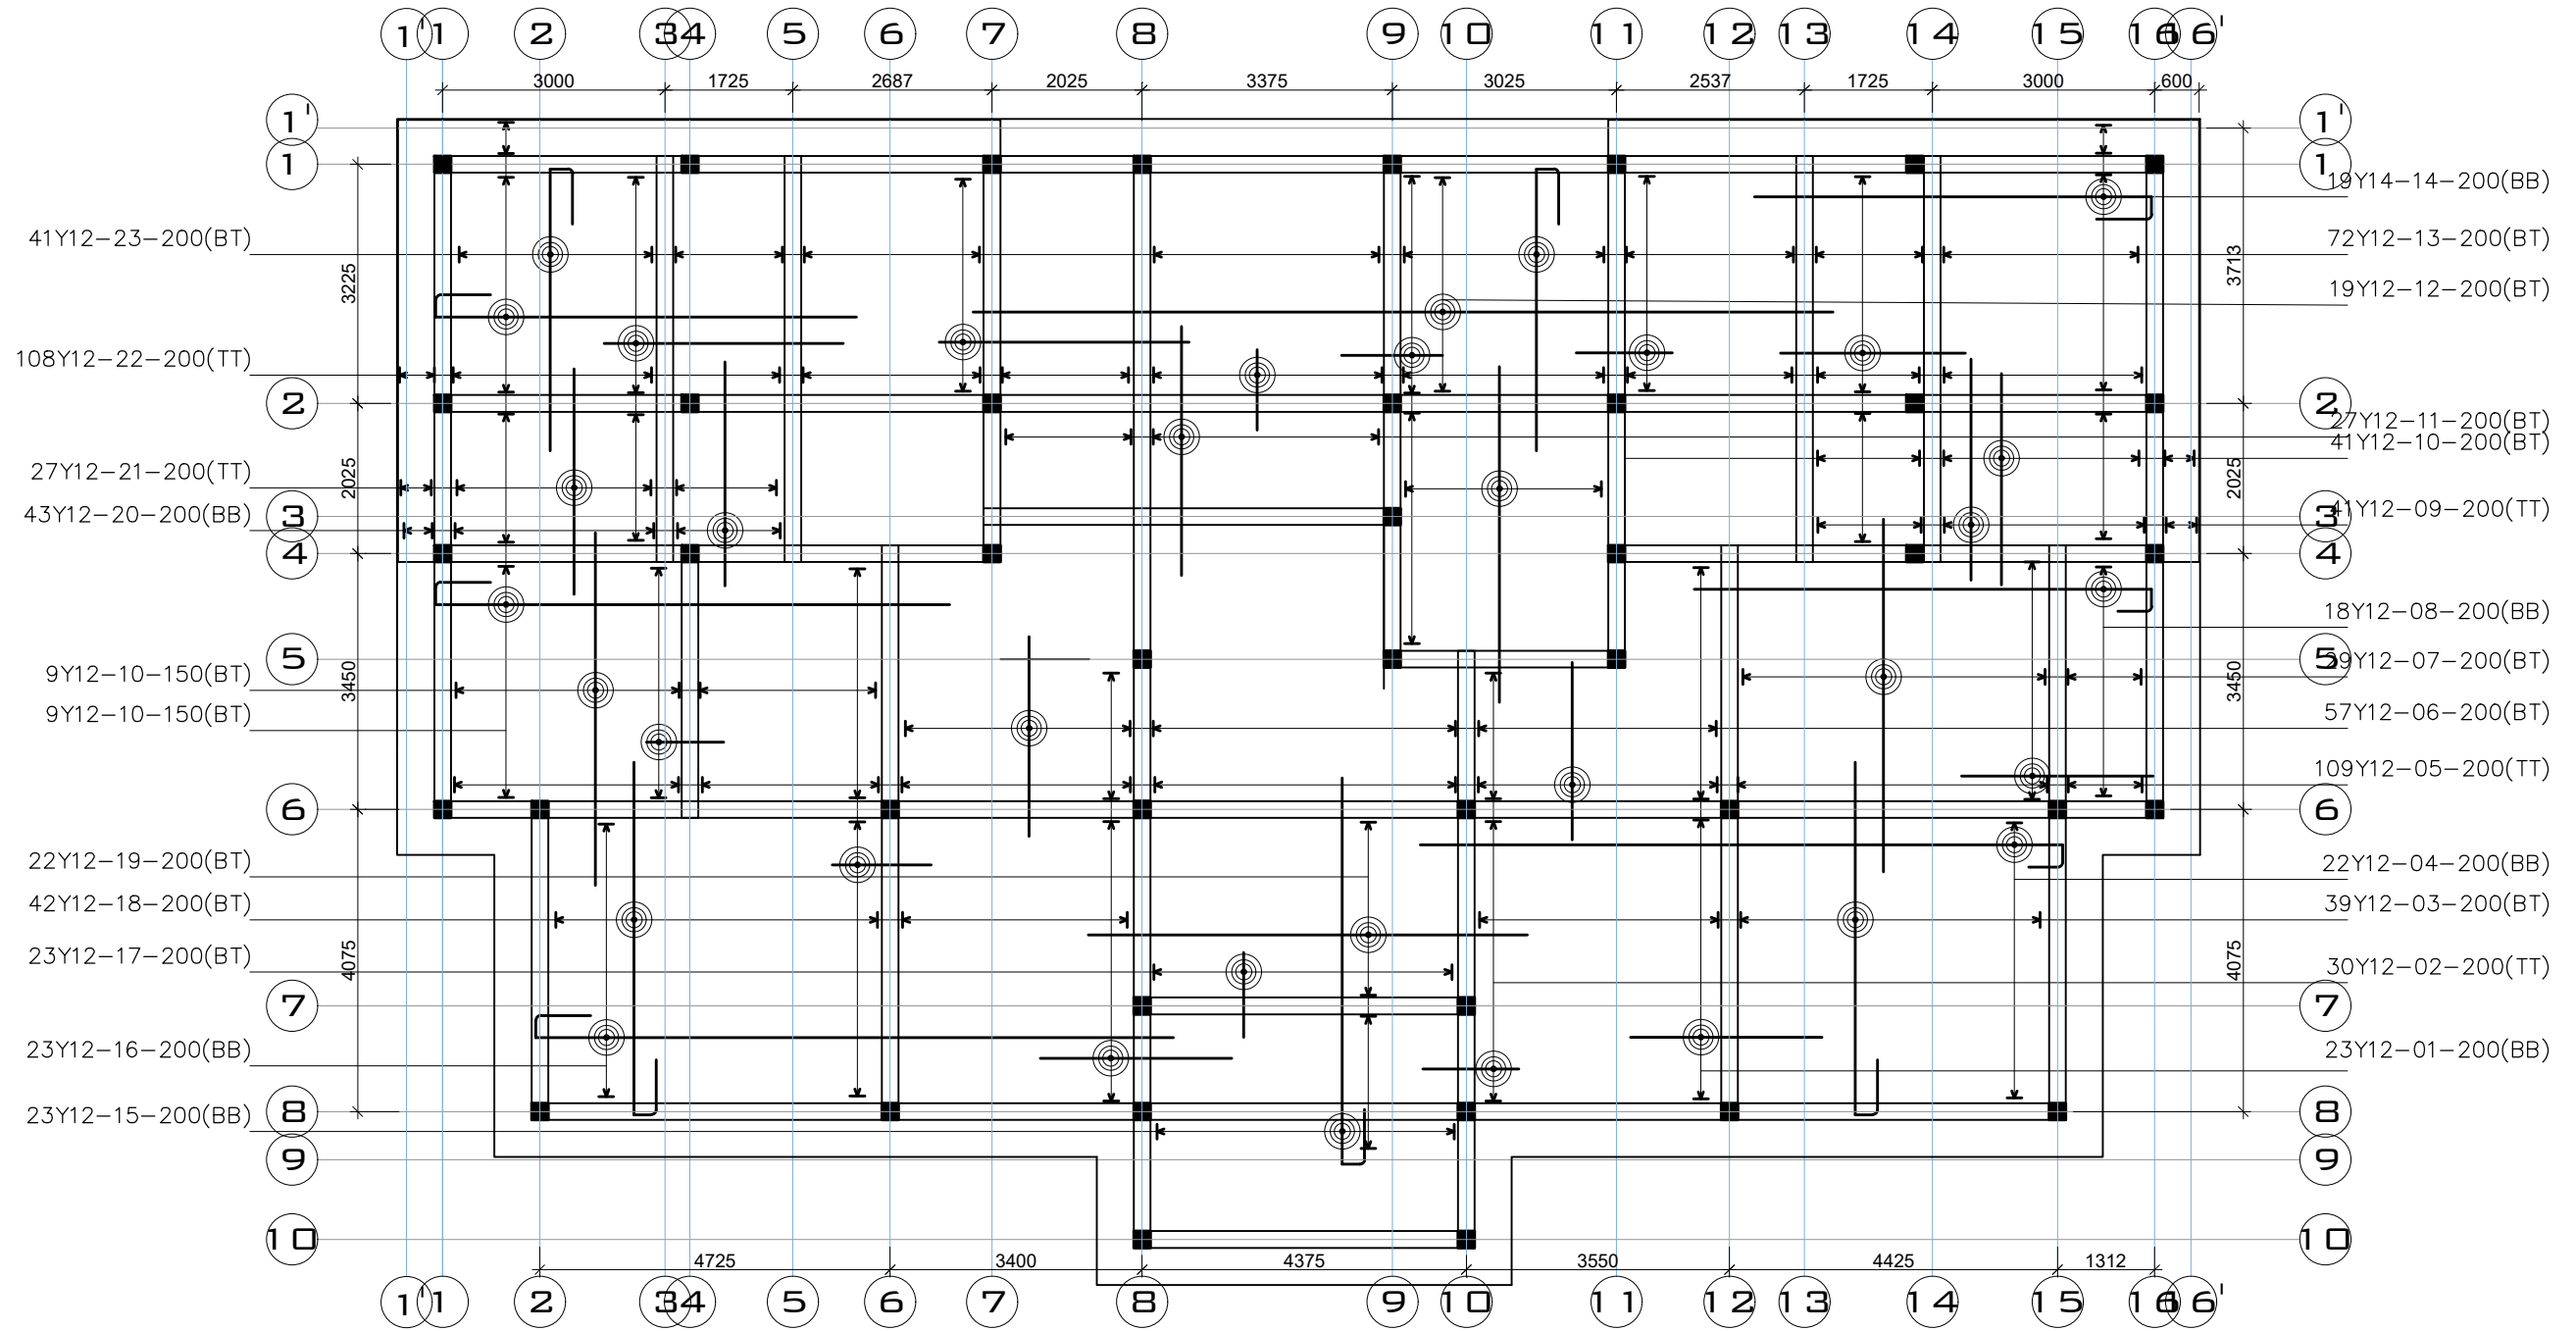

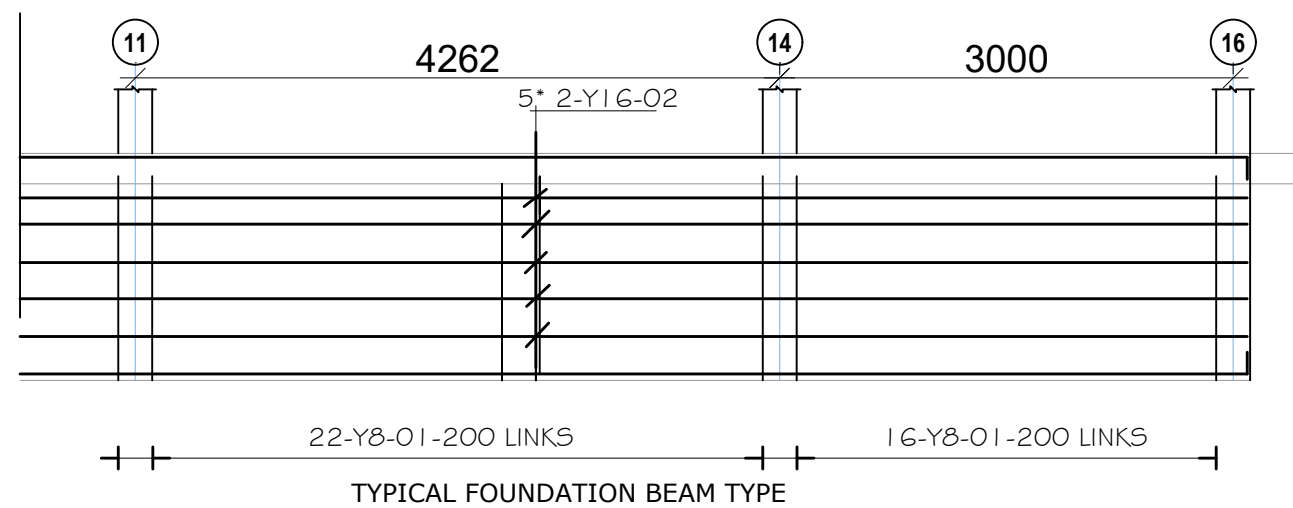

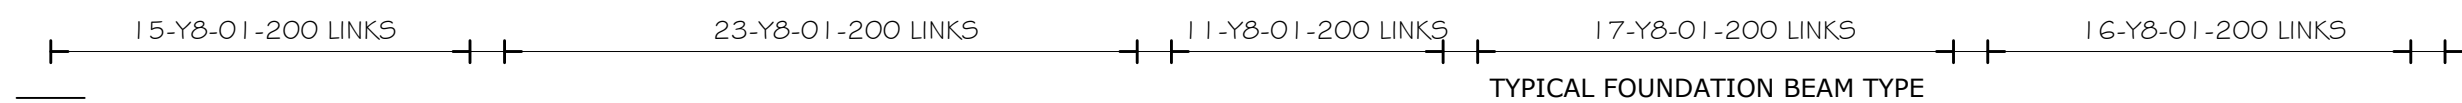

RAFT FOUNDATION SLAB SECTION

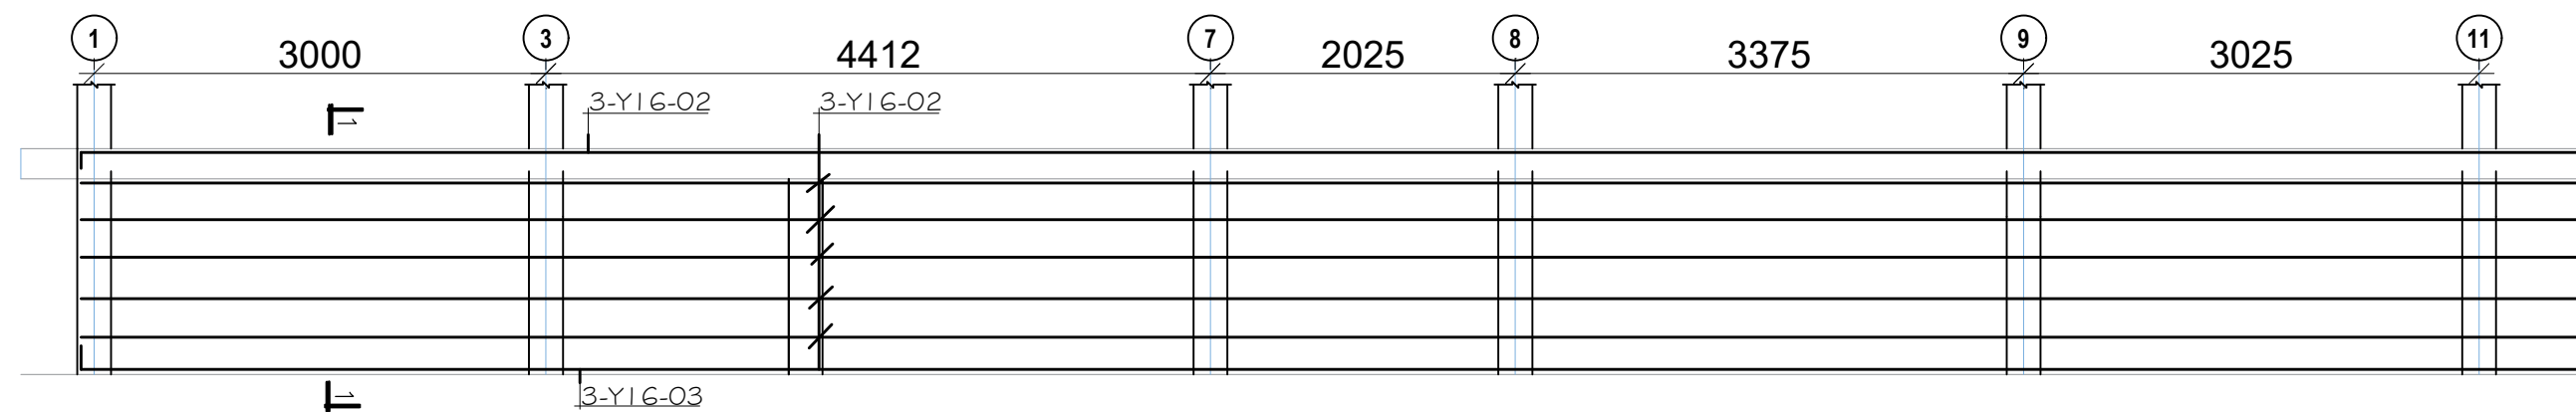