







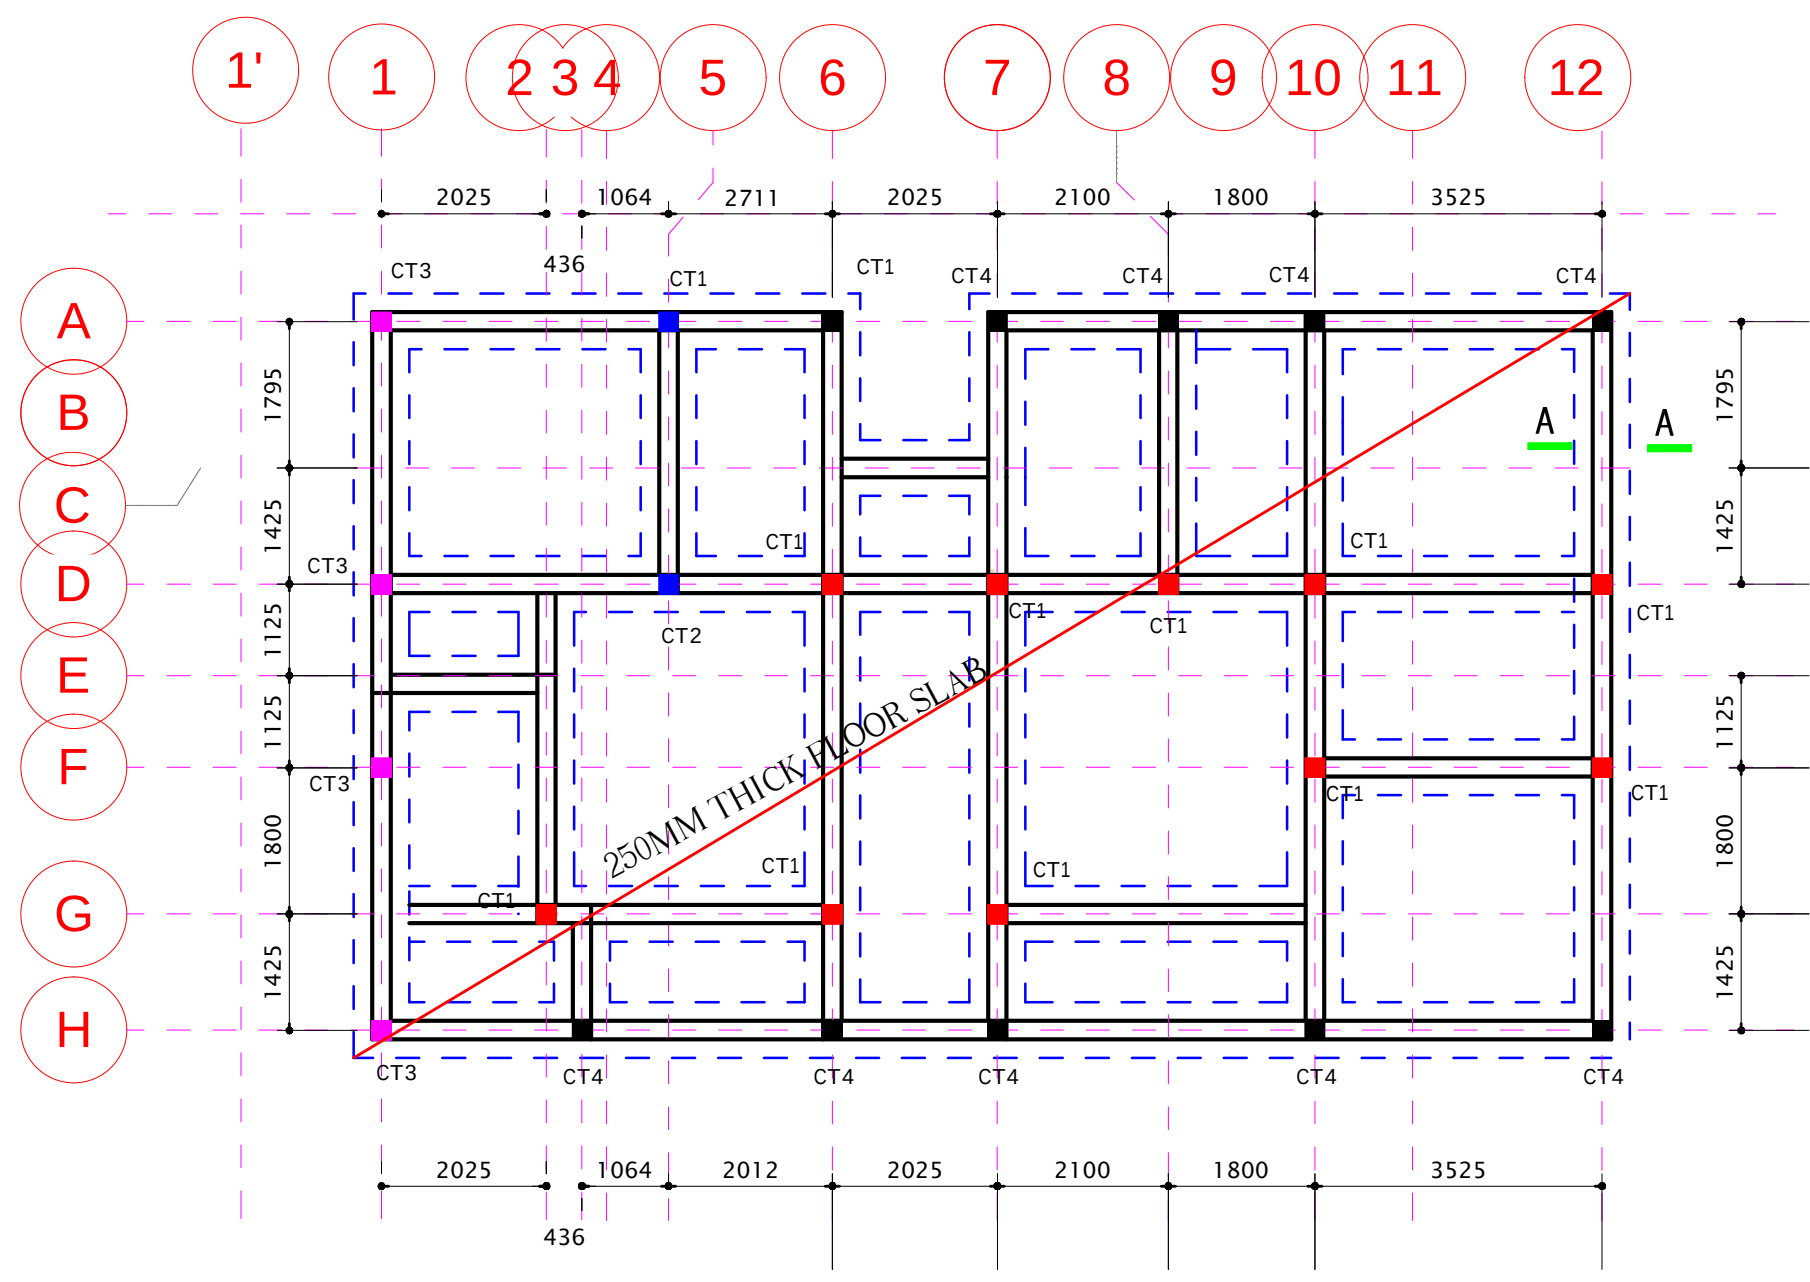


APPROVAL COLUMN

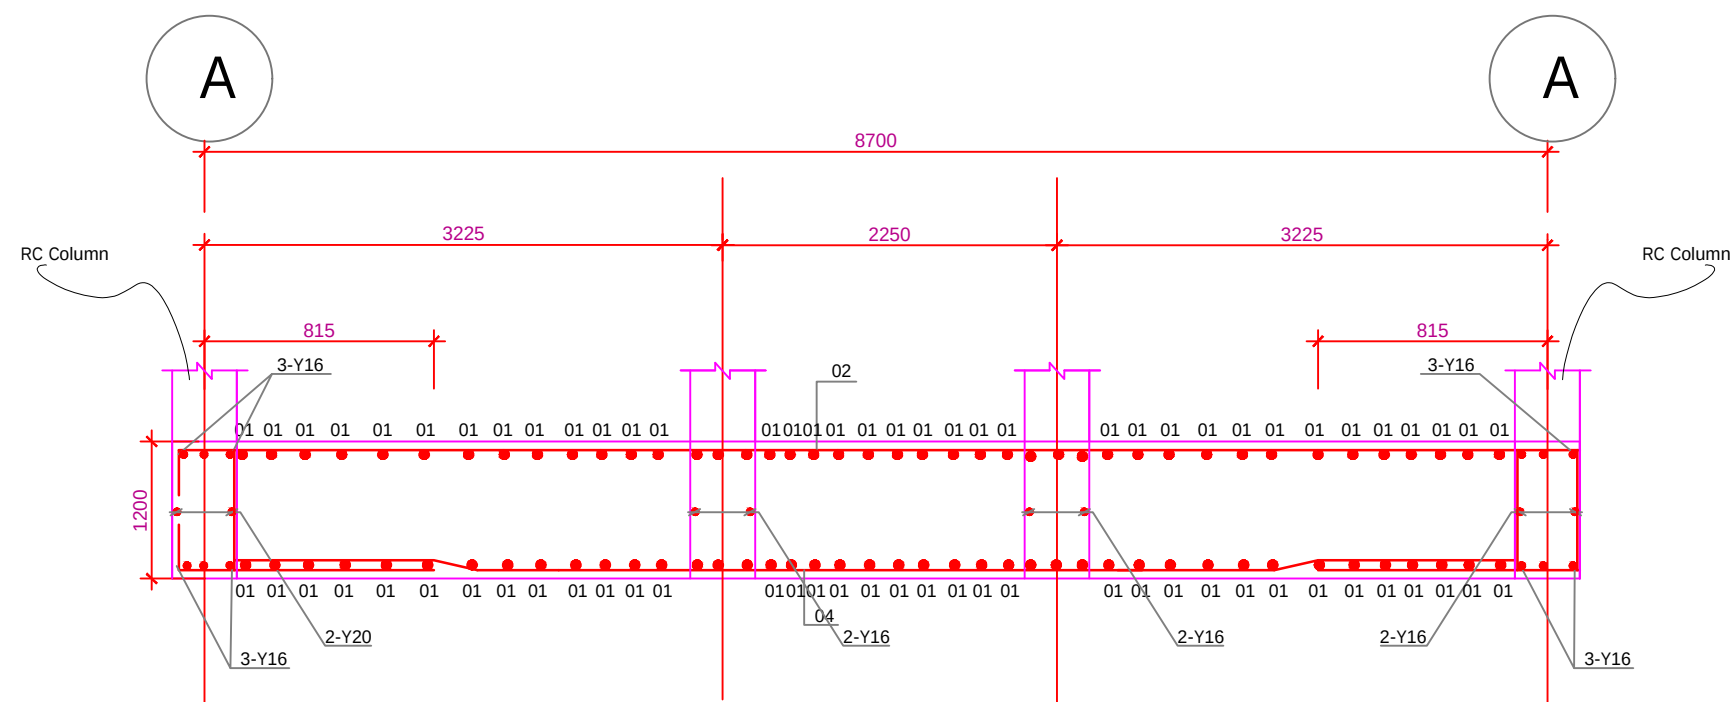

RAFT SLAB SECTION A-A.

APPROVAL COLUMN

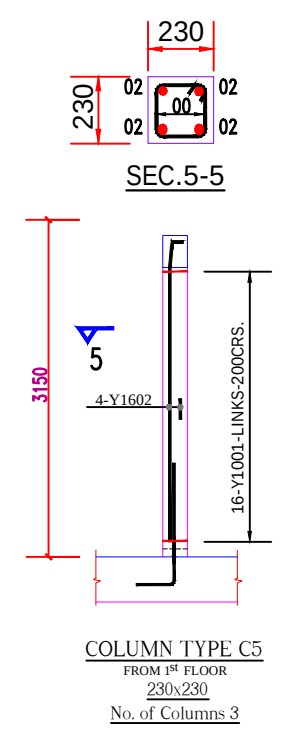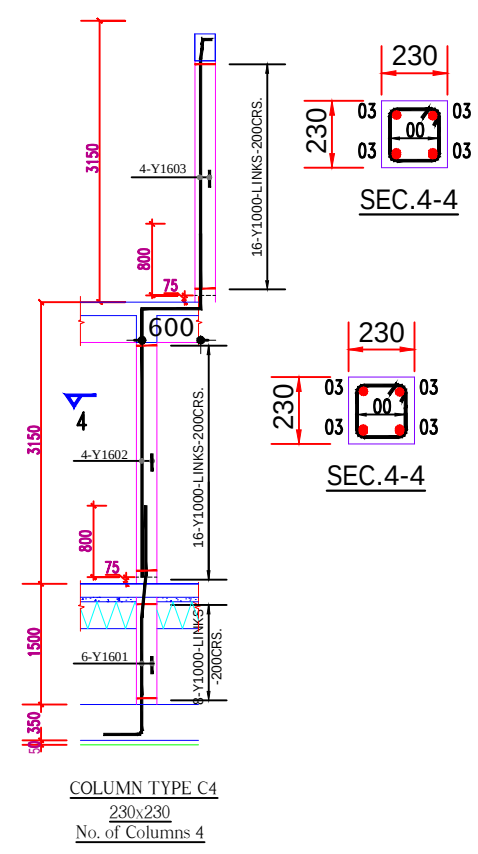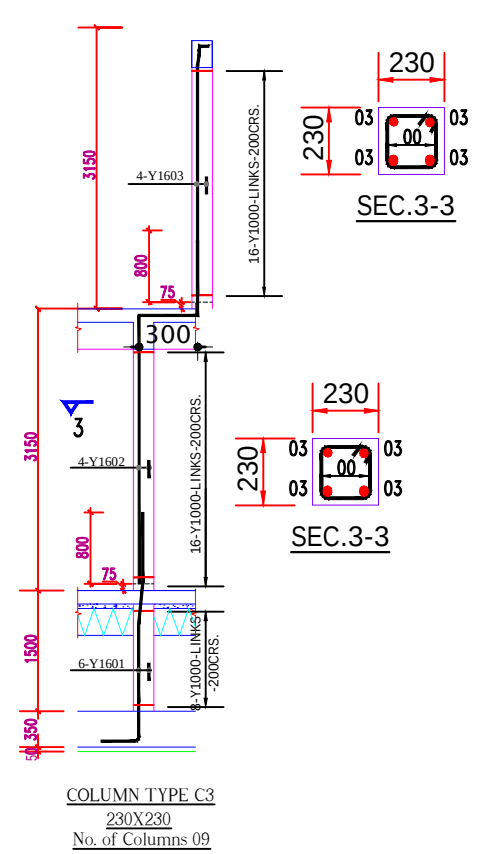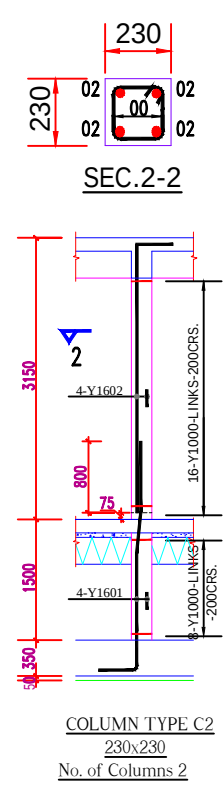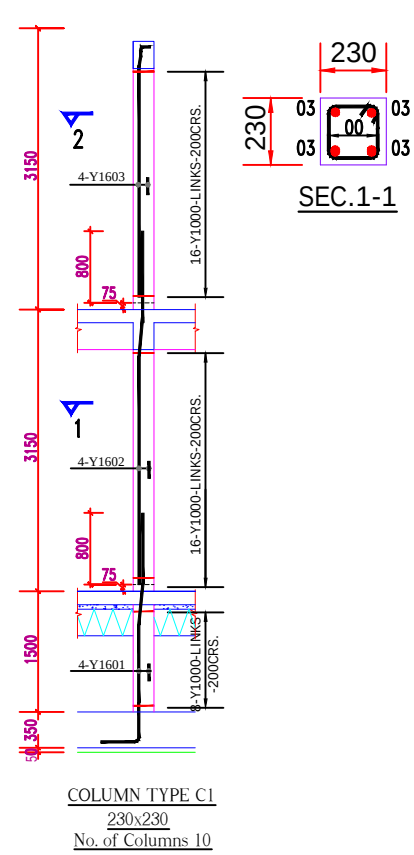

APPROVAL COLUMN