




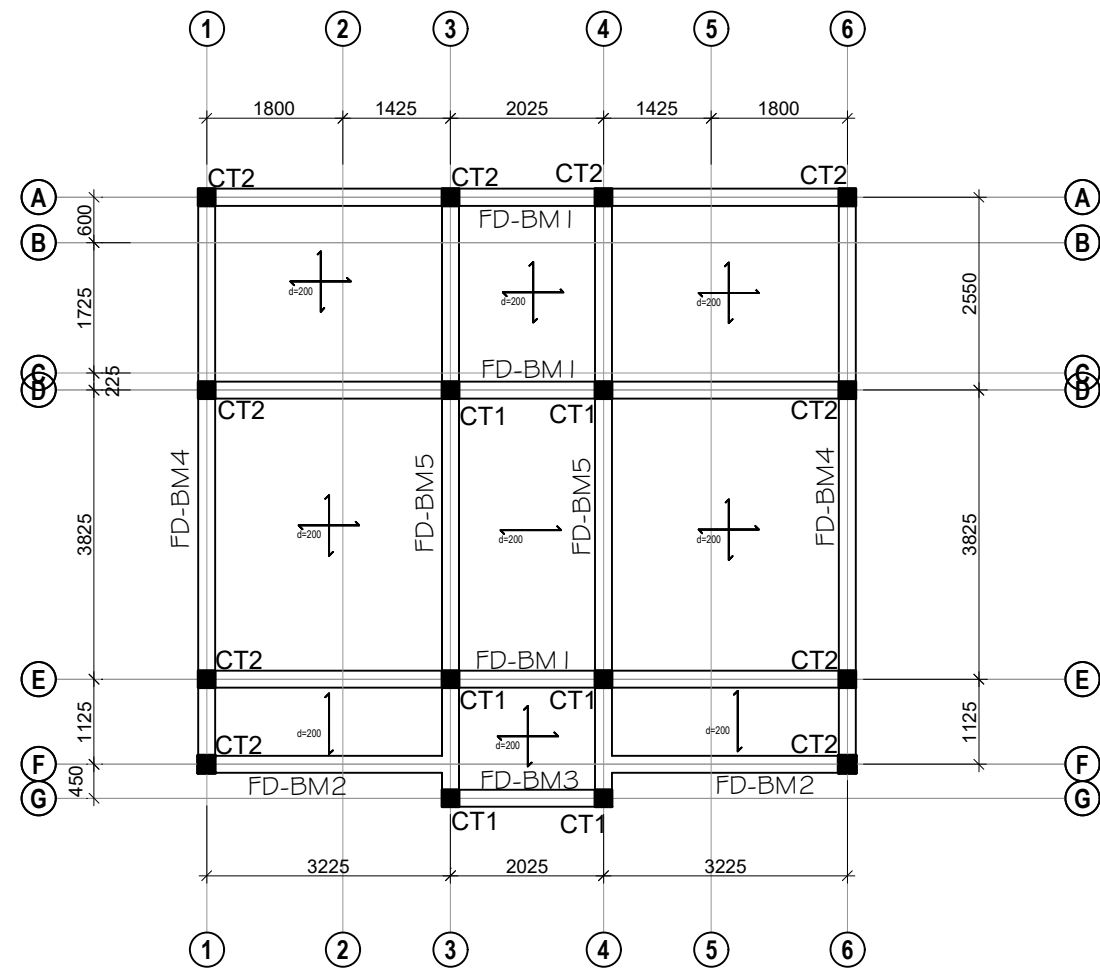


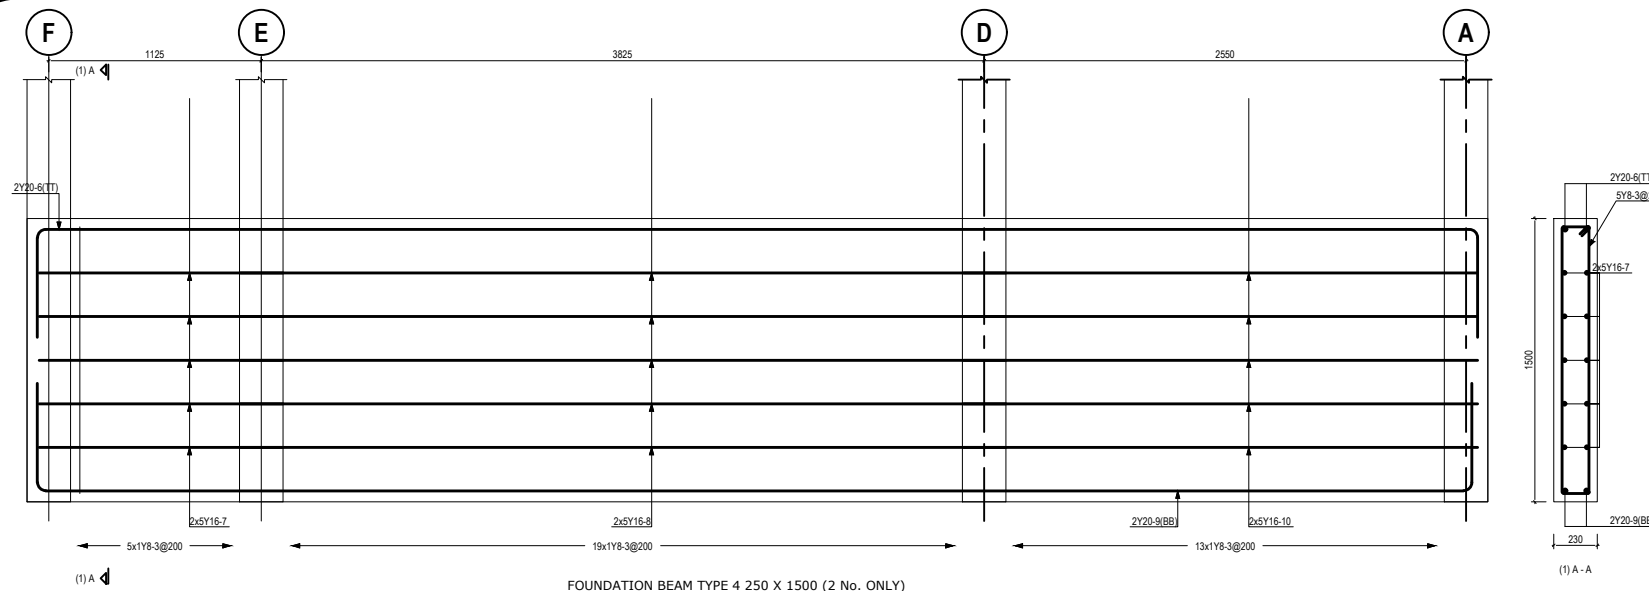


FOUNDATION BEAM TYPE 4 250 X 1500 (2 No. ONLY)

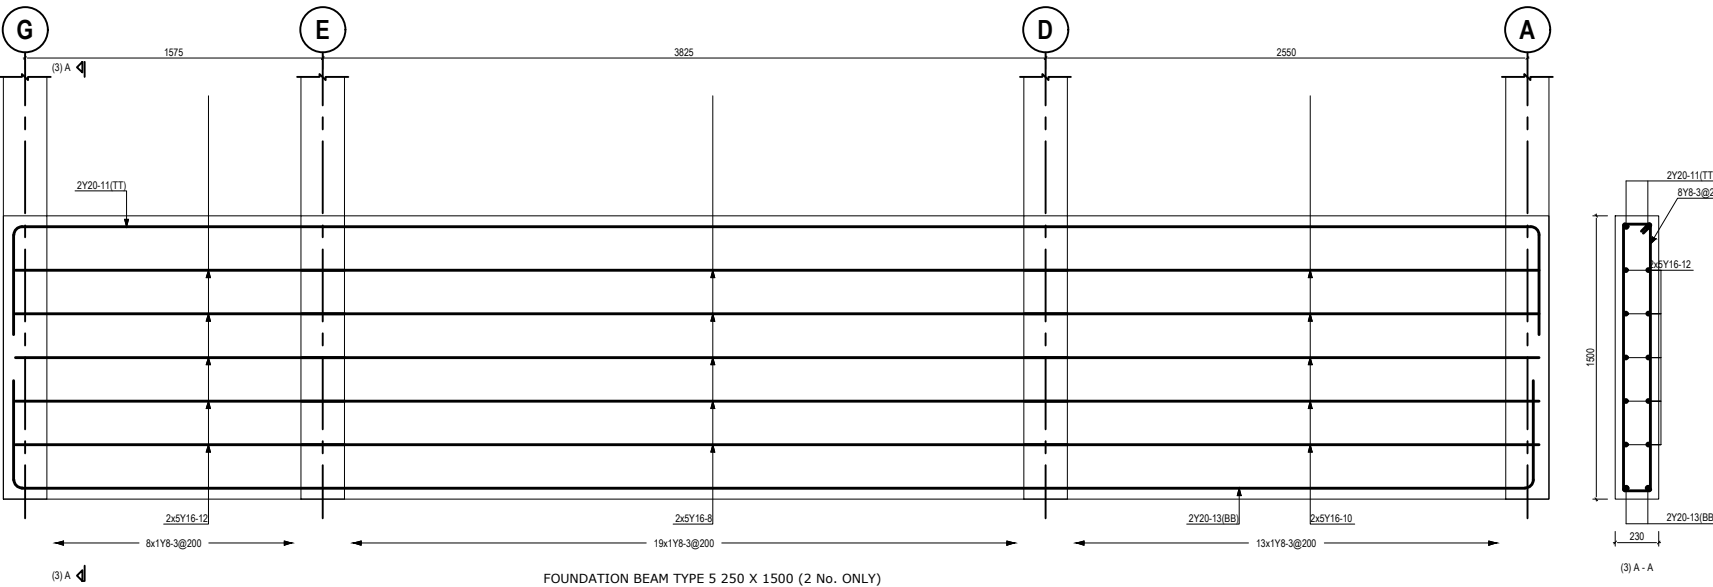


FOUNDATION BEAM TYPE 5 250 X 1500 (2 No. ONLY)

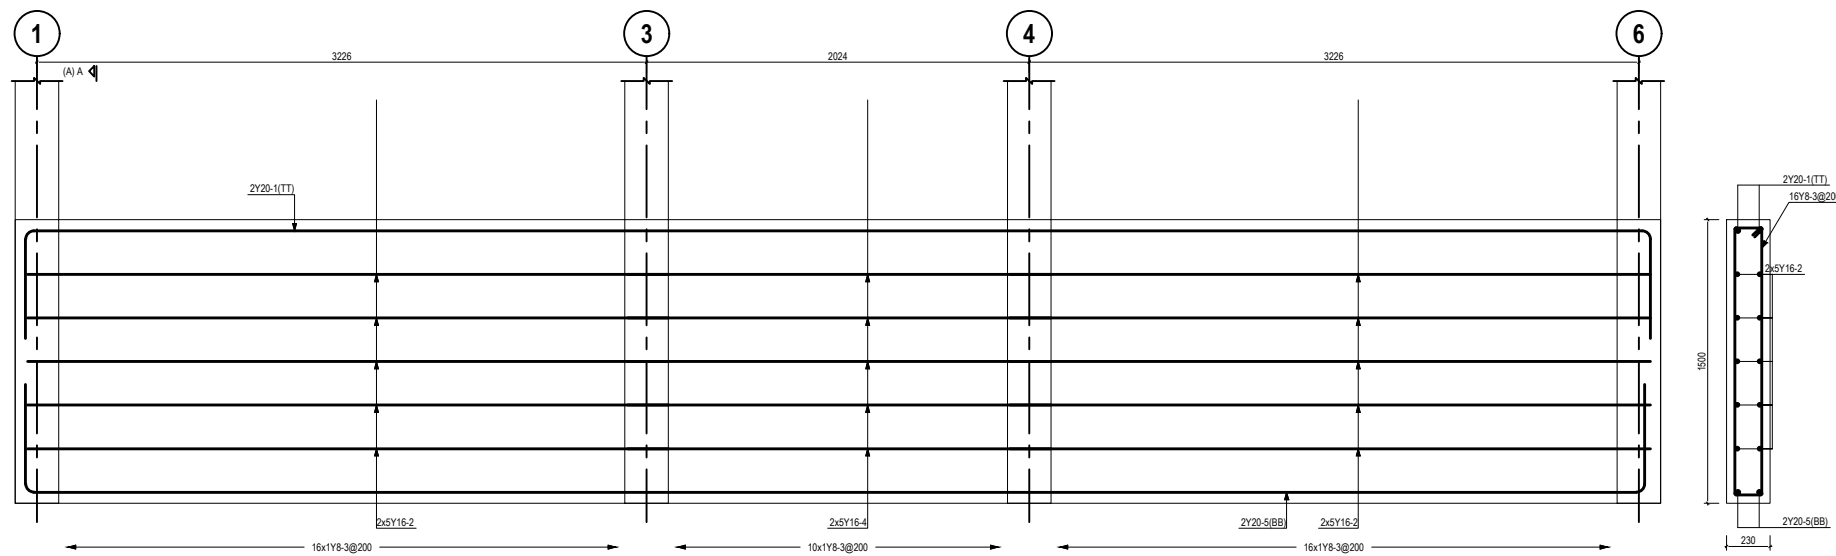







FOUNDATION BEAM TYPE 3 250 X 1000 (1 No. ONLY)

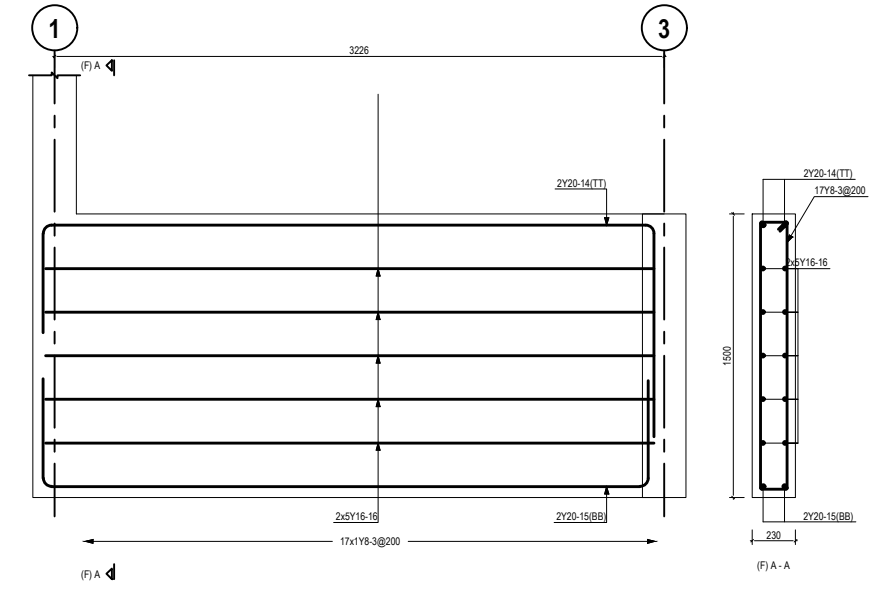

FOUNDATION BEAM TYPE 2 250 X 1500 (2 No. ONLY)

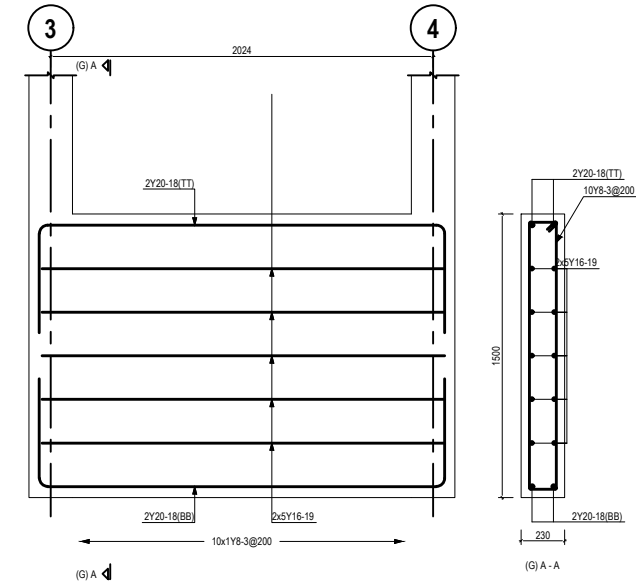

FOUNDATION BEAM TYPE 3 250 X 1000 (1 No. ONLY)

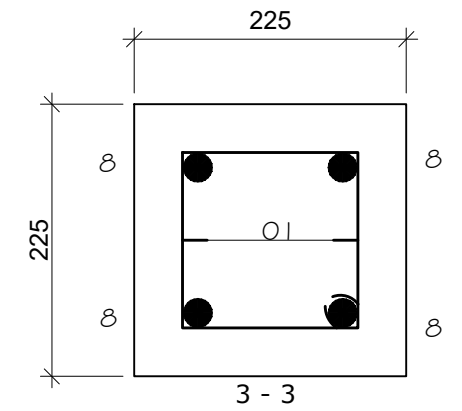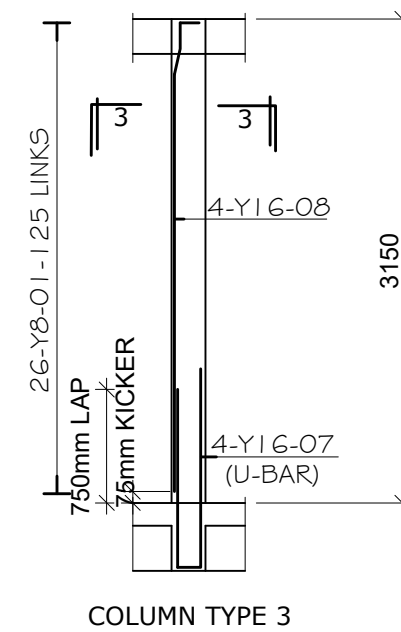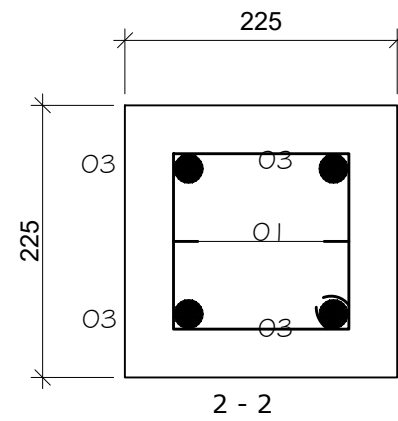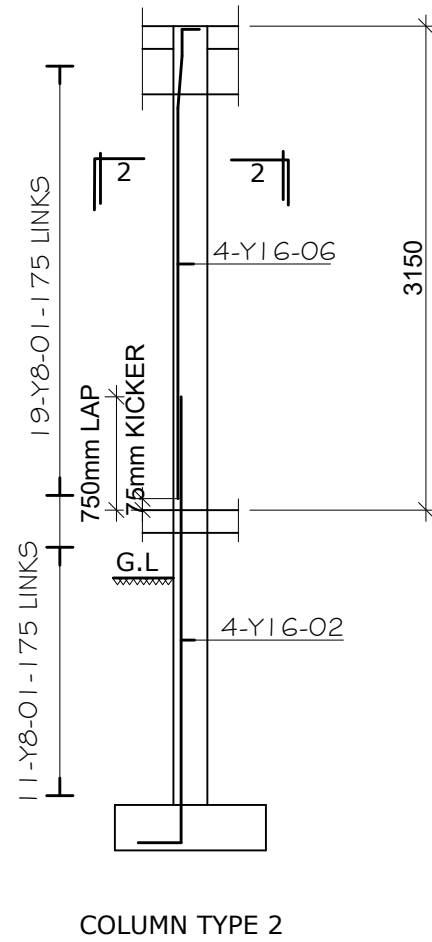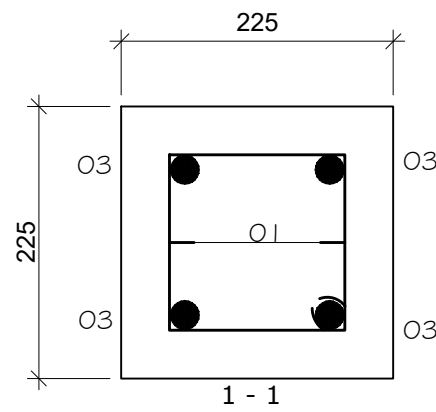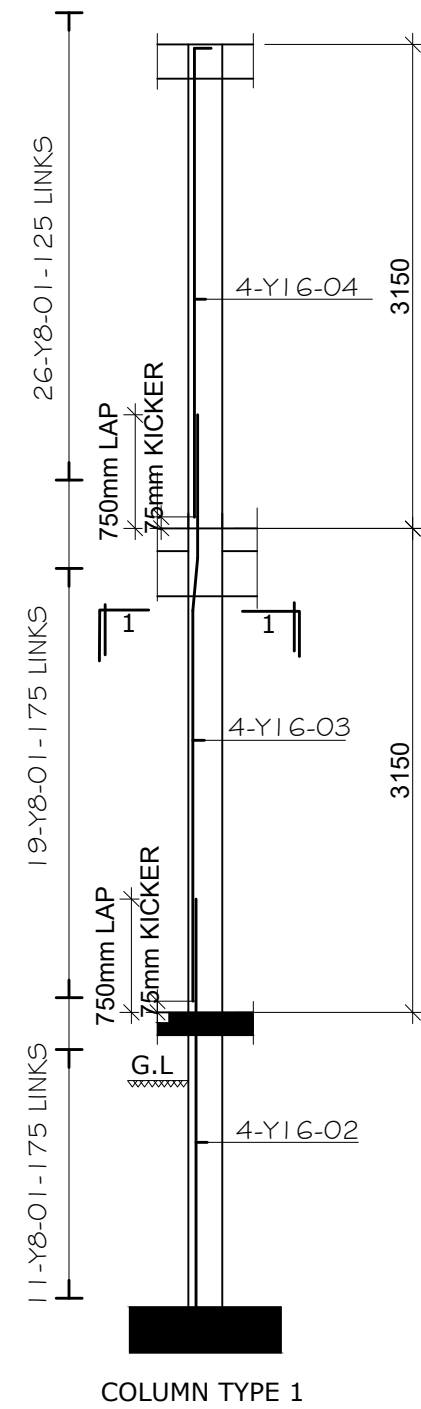

SCHEDULE OF LINTELS

	Depth (mm)	Reinforcement		Links
		Top	Bottom	
$l \leq 1.2\text{m}$	225	2Y12	2Y12	6mm Ø bar @ 200
$l \leq 2.0\text{m}$	225	2Y12	2Y12	6mm Ø bar @ 200
$l \leq 3.0\text{m}$	225	2Y12	2Y12	6mm Ø bar @ 200
$l \leq 4.0\text{m}$	300	2Y12	3Y12	6mm Ø bar @ 200
$l \leq 5.0\text{m}$	300	2Y12	2Y16	8mm Ø bar @ 200
$l \leq 6.0\text{m}$	450	2Y12	2Y16	8mm Ø bar @ 200